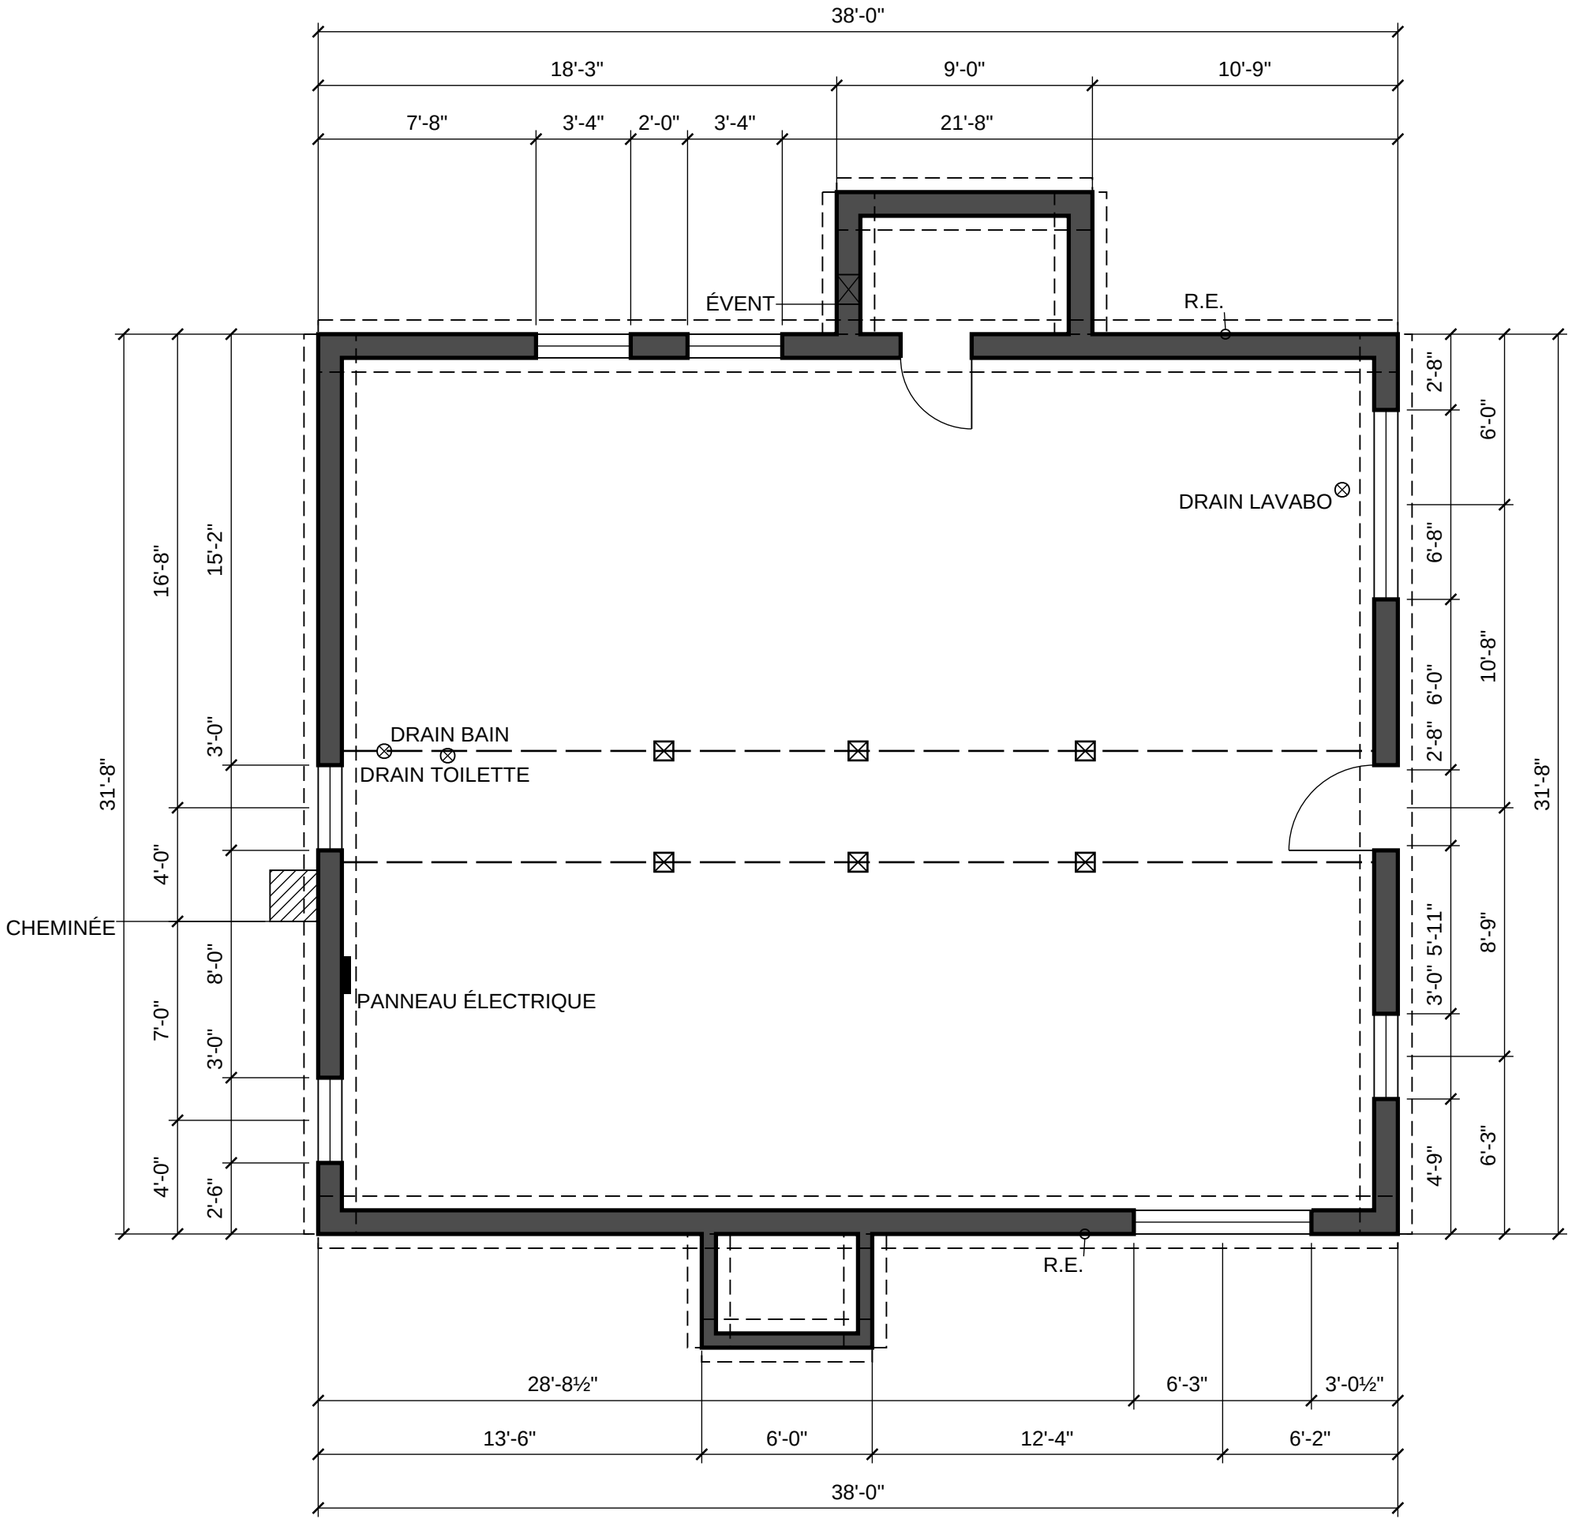


FAÇADE AVANT (RUE)

PROJET

Résidence — 86, avenue Laurier, Baie-Comeau

RELEVÉ DE L'EXISTANT — PRÉLIMINAIRE, À VALIDER SUR PLACE

LÉGENDE

- Mur extérieur / fondation
- Mur intérieur (cloison)
- Poutre (au-dessus)
- Axe porteur d'origine
- Colonne
- Solives (sens)
- ≈ Valeur estimée (mesurée sur l'image)
- ⚠n Voir registre des écarts dans RAPPORT.md
- Cotes en pieds-pouces
- Noms, dimensions et superficies des pièces : voir tableau_pieces.csv

NOTES DU PLAN D'ORIGINE (traduites)

1. Solives de plancher 2 po × 10 po espacées de 20 po c/c (plancher du RDC), parallèles à y. [« SOLIVES 2"x10" @ 20" c/c »]
2. Solives doublées sous les cloisons parallèles aux solives (un double trait dessiné à x ≈ 137, de la poutre arrière au mur arrière). [« SOLIVES DOUBLES SOUS LES CLOISONS PARALLÈLES »]
3. Rangées d'entretoises en croix entre les solives (dessinées dans la moitié gauche seulement). [« CROIX ST ANDRÉ (3 fois) »]
4. Deux poutres de 8 × 10 po sur colonnes de bois de 8 × 8 po (3 par poutre). [« POUTRE 8"x10" (2 fois) ; COL. BOIS, 8"x8" »]

… autres notes : voir maison.json

NORD
9,8° (sens horaire depuis +y).
Source : ESTIMÉ (P7)

ÉCHELLE GRAPHIQUE (pi)


0 4 8 12 pi

PHOTOS SOURCES
P2, P3

ÉCHELLE	DATE	RÉVISION
3/16" = 1'-0"	2026-10-29	R0

NIVEAU
SOUS-SOL

FEUILLE
A-100

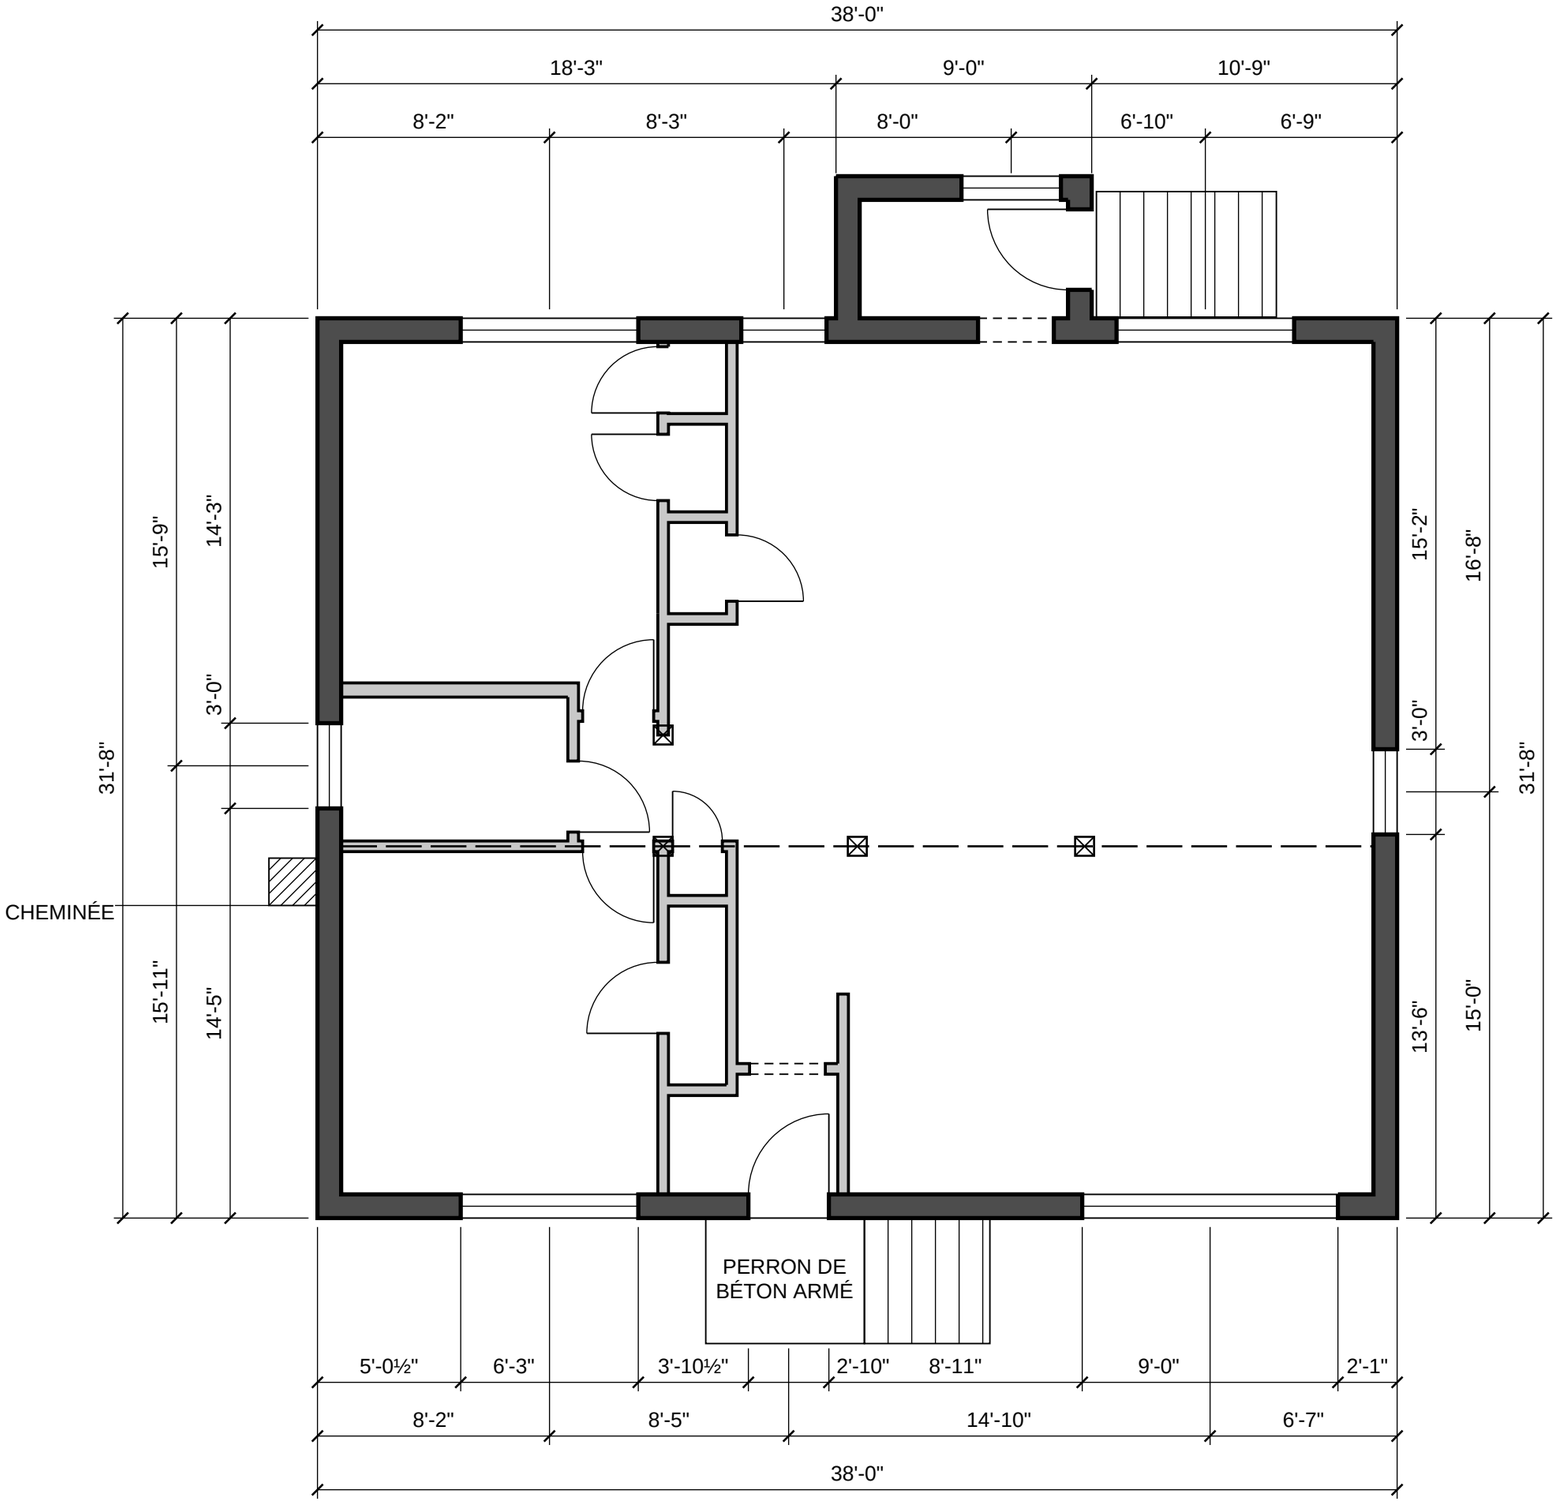

FAÇADE AVANT (RUE)

PROJET

Résidence — 86, avenue Laurier, Baie-Comeau

RELEVÉ DE L'EXISTANT — PRÉLIMINAIRE, À VALIDER SUR PLACE

LÉGENDE

- Mur extérieur / fondation
- Mur intérieur (cloison)
- Poutre (au-dessus)
- Axe porteur d'origine
- Colonne
- Solives (sens)
- ≈ Valeur estimée (mesurée sur l'image)
- ⚠n Voir registre des écarts dans RAPPORT.md
- Cotes en pieds-pouces
- Noms, dimensions et superficies des pièces : voir tableau_pieces.csv

NOTES DU PLAN D'ORIGINE (traduites)

1. Tringle et tablette dans toutes les garde-robes. [« NOTE : BARRE & TABLETTE DANS TOUS LES G.R. »]
2. Perron avant en béton armé de barres de ½ po à 10 po c/c. [« BÉTON REN. AVEC BARRE ½"Ø @ 10" c/c »]

NORD

N

9,8° (sens horaire depuis +y).
Source : ESTIMÉ (P7)

ÉCHELLE GRAPHIQUE (pi)

0 4 8 12 pi

PHOTOS SOURCES

P4, P5, P6

ÉCHELLE	DATE	RÉVISION
3/16" = 1'-0"	2026-10-29	R0

NIVEAU

REZ-DE-CHAUSSÉE

FEUILLE

A-101