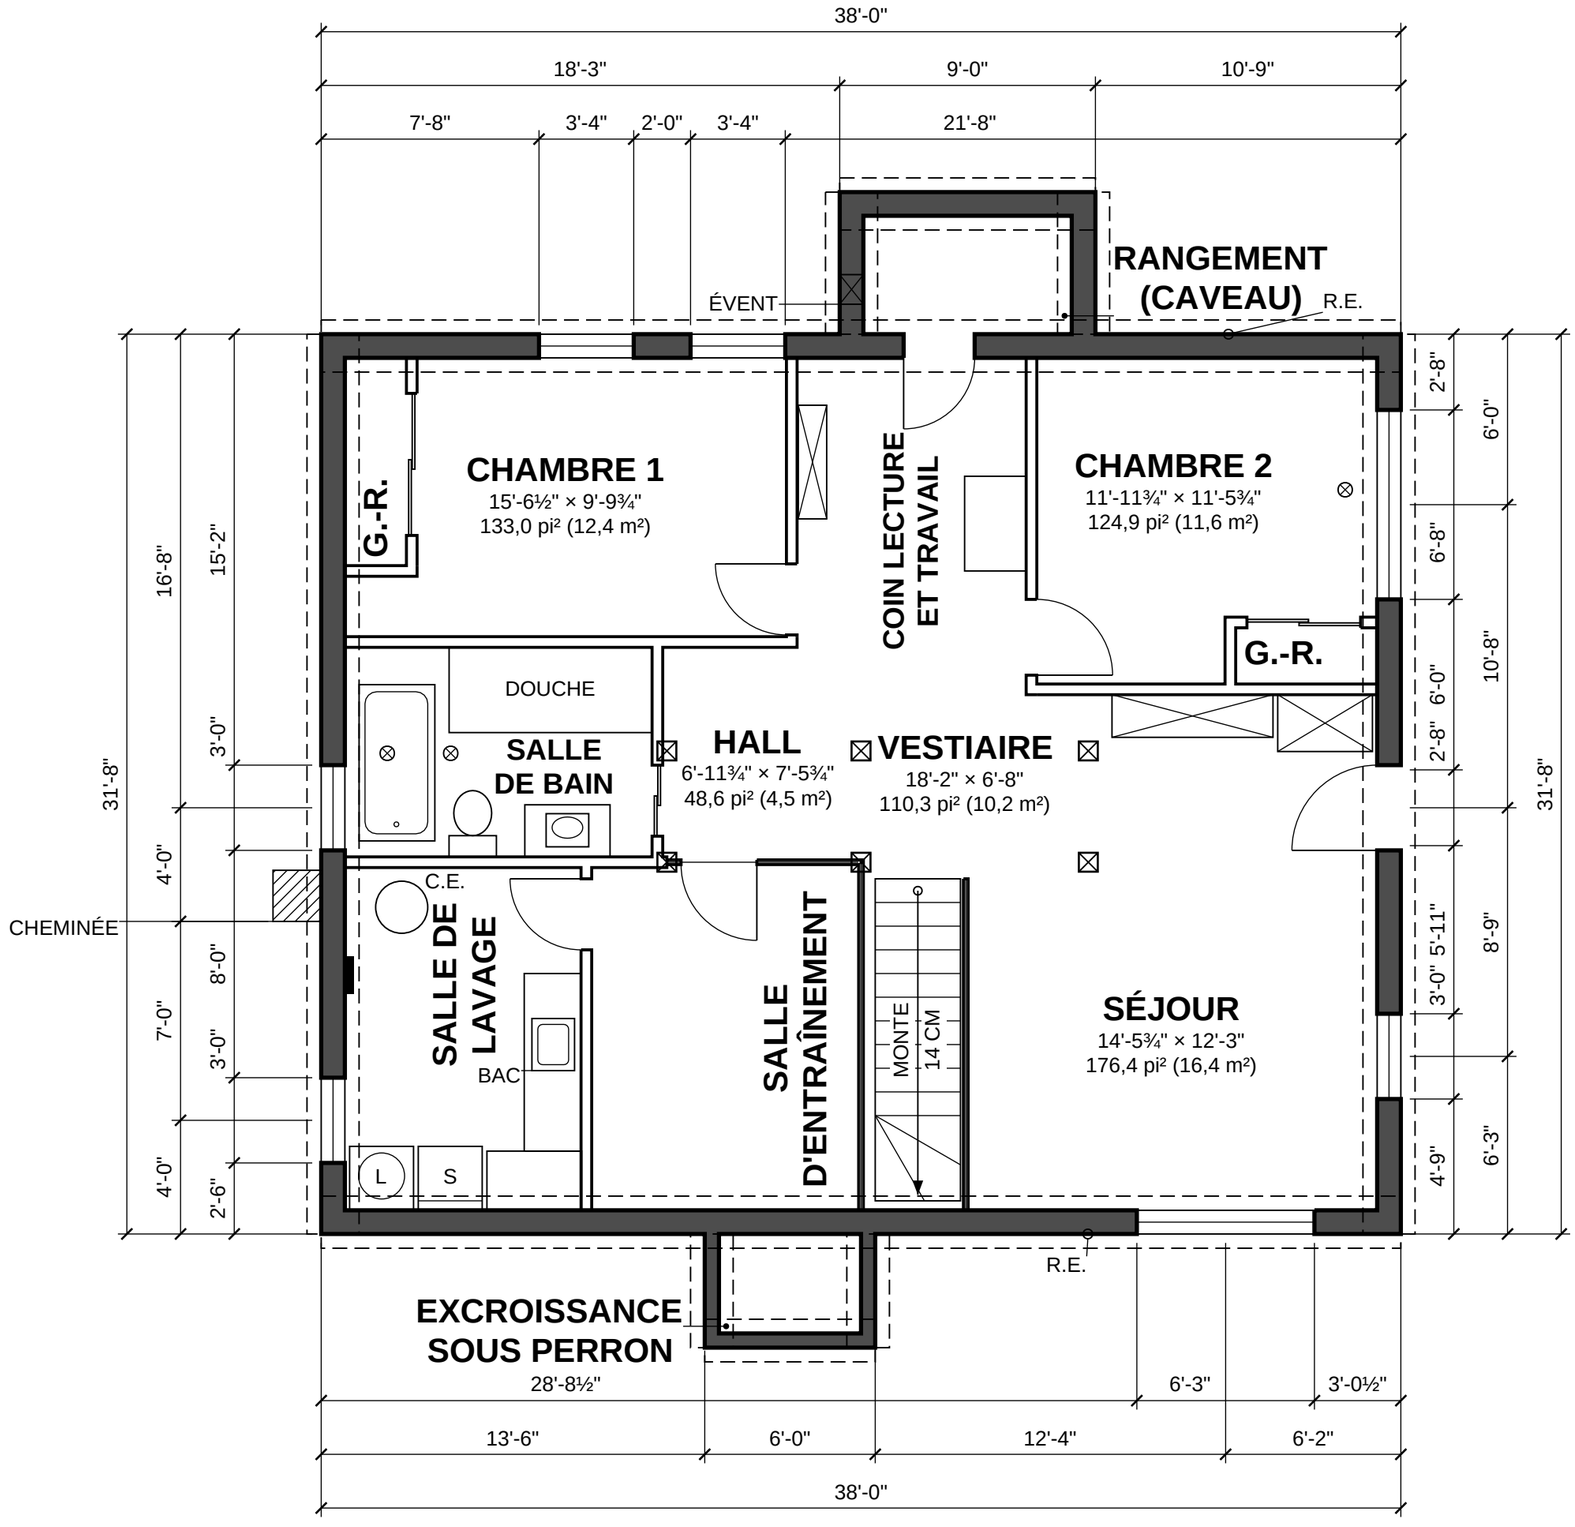


FAÇADE AVANT (RUE)

PROJET

Résidence — 86, avenue Laurier, Baie-Comeau

PROPOSITION SS-14 — COIN LECTURE, BAC DE LA SALLE DE LAVAGE — ESQUISSE À VALIDER

LÉGENDE

- Mur extérieur / fondation
- Mur intérieur existant
- Cloison projetée (nouvelle)
- Cloison vitrée projetée
- ⊠ Colonne
- ≈ Valeur estimée (mesurée sur l'image)
- ⚠n Voir registre des écarts dans RAPPORT.md
- Cotes en pieds-pouces
- ⊗ Drain
- ▬ Panneau électrique
- Petites pièces : nom seul ; dimensions et superficie dans tableau_pieces.csv

NOTES DE LA PROPOSITION

1. Esquisse : cloisons, portes, escalier, bar et appareils projetés ; le reste est l'existant (base R0).
2. Escalier de 14 c.m. à l'entrée avant (voir P-122) : trémie, giron et échappée à valider.
3. Escalier flottant (limon central acier, marches de chêne) ; garde vitrée côté séjour.
4. Salle de bain refaite : vanité simple, douche de 7 pi, bain autoportant (drains à déplacer).
5. Coin lecture et travail ouvert : bureau, pouf, petite bibliothèque basse.
6. Hauteur du sous-sol : 8 pi (propriétaire) ; hauteur sous poutres et coupe-feu à valider.

NORD

9,8° (sens horaire depuis +y).
Source : ESTIMÉ (P7)

ÉCHELLE GRAPHIQUE (pi)

0 — 4 — 8 — 12 pi

PHOTOS SOURCES

P2, P3


ÉCHELLE	DATE	RÉVISION
3/16" = 1'-0"	2026-10-29	A

NIVEAU

SOUS-SOL PROPOSÉ

FEUILLE

P-121

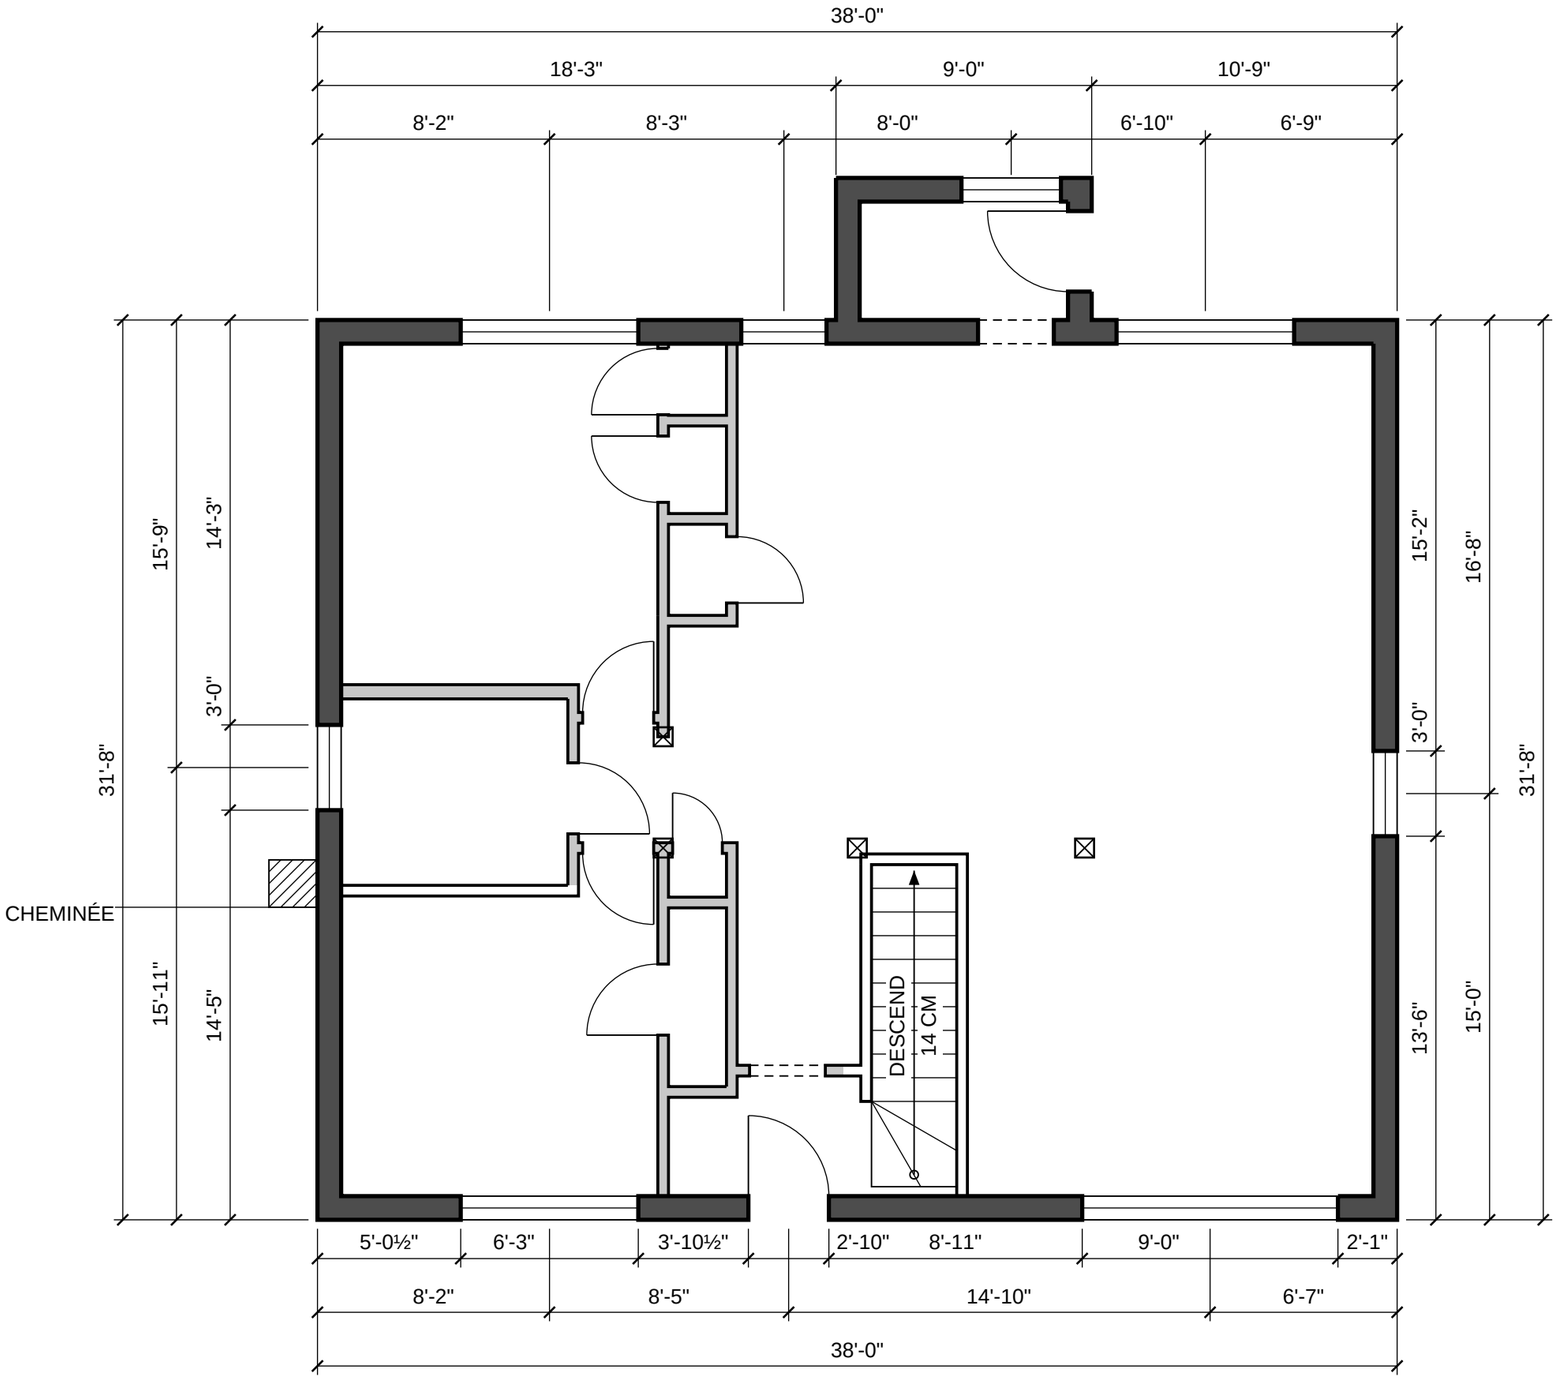

FAÇADE AVANT (RUE)

PROJET

Résidence — 86, avenue Laurier, Baie-Comeau

PROPOSITION SS-14 — COIN LECTURE, BAC DE LA SALLE DE LAVAGE — ESQUISSE À VALIDER

LÉGENDE

- Mur extérieur / fondation
- Mur intérieur existant
- Cloison projetée (nouvelle)
- ⊠ Colonne
- ≈ Valeur estimée (mesurée sur l'image)
- ⚠n Voir registre des écarts dans RAPPORT.md
- Cotes en pieds-pouces

NOTES DE LA PROPOSITION

1. Escalier à l'entrée avant (option 2) : trémie d'environ 3 × 10 pi à ouvrir dans le plancher.
2. Vestibule d'entrée commun : on descend au sous-sol ou on entre au logement du haut.
3. Cloison entre l'entrée et le salon enlevée ; cage fermée côté salon et côté hall.
4. Porte d'entrée : pentures à gauche (sens inversé) ; coupe-feu entre logements à valider.
5. Salle de bain agrandie de 1½ pi vers la chambre avant (mur déplacé) ; plomberie à vérifier.

NORD
9,8° (sens horaire depuis +y).
Source : ESTIMÉ (P7)

ÉCHELLE GRAPHIQUE (pi)

0 — 4 — 8 — 12 pi

PHOTOS SOURCES
P4, P5, P6

ÉCHELLE	DATE	RÉVISION
3/16" = 1'-0"	2026-10-29	A

NIVEAU
RDC PROPOSÉ

FEUILLE
P-122