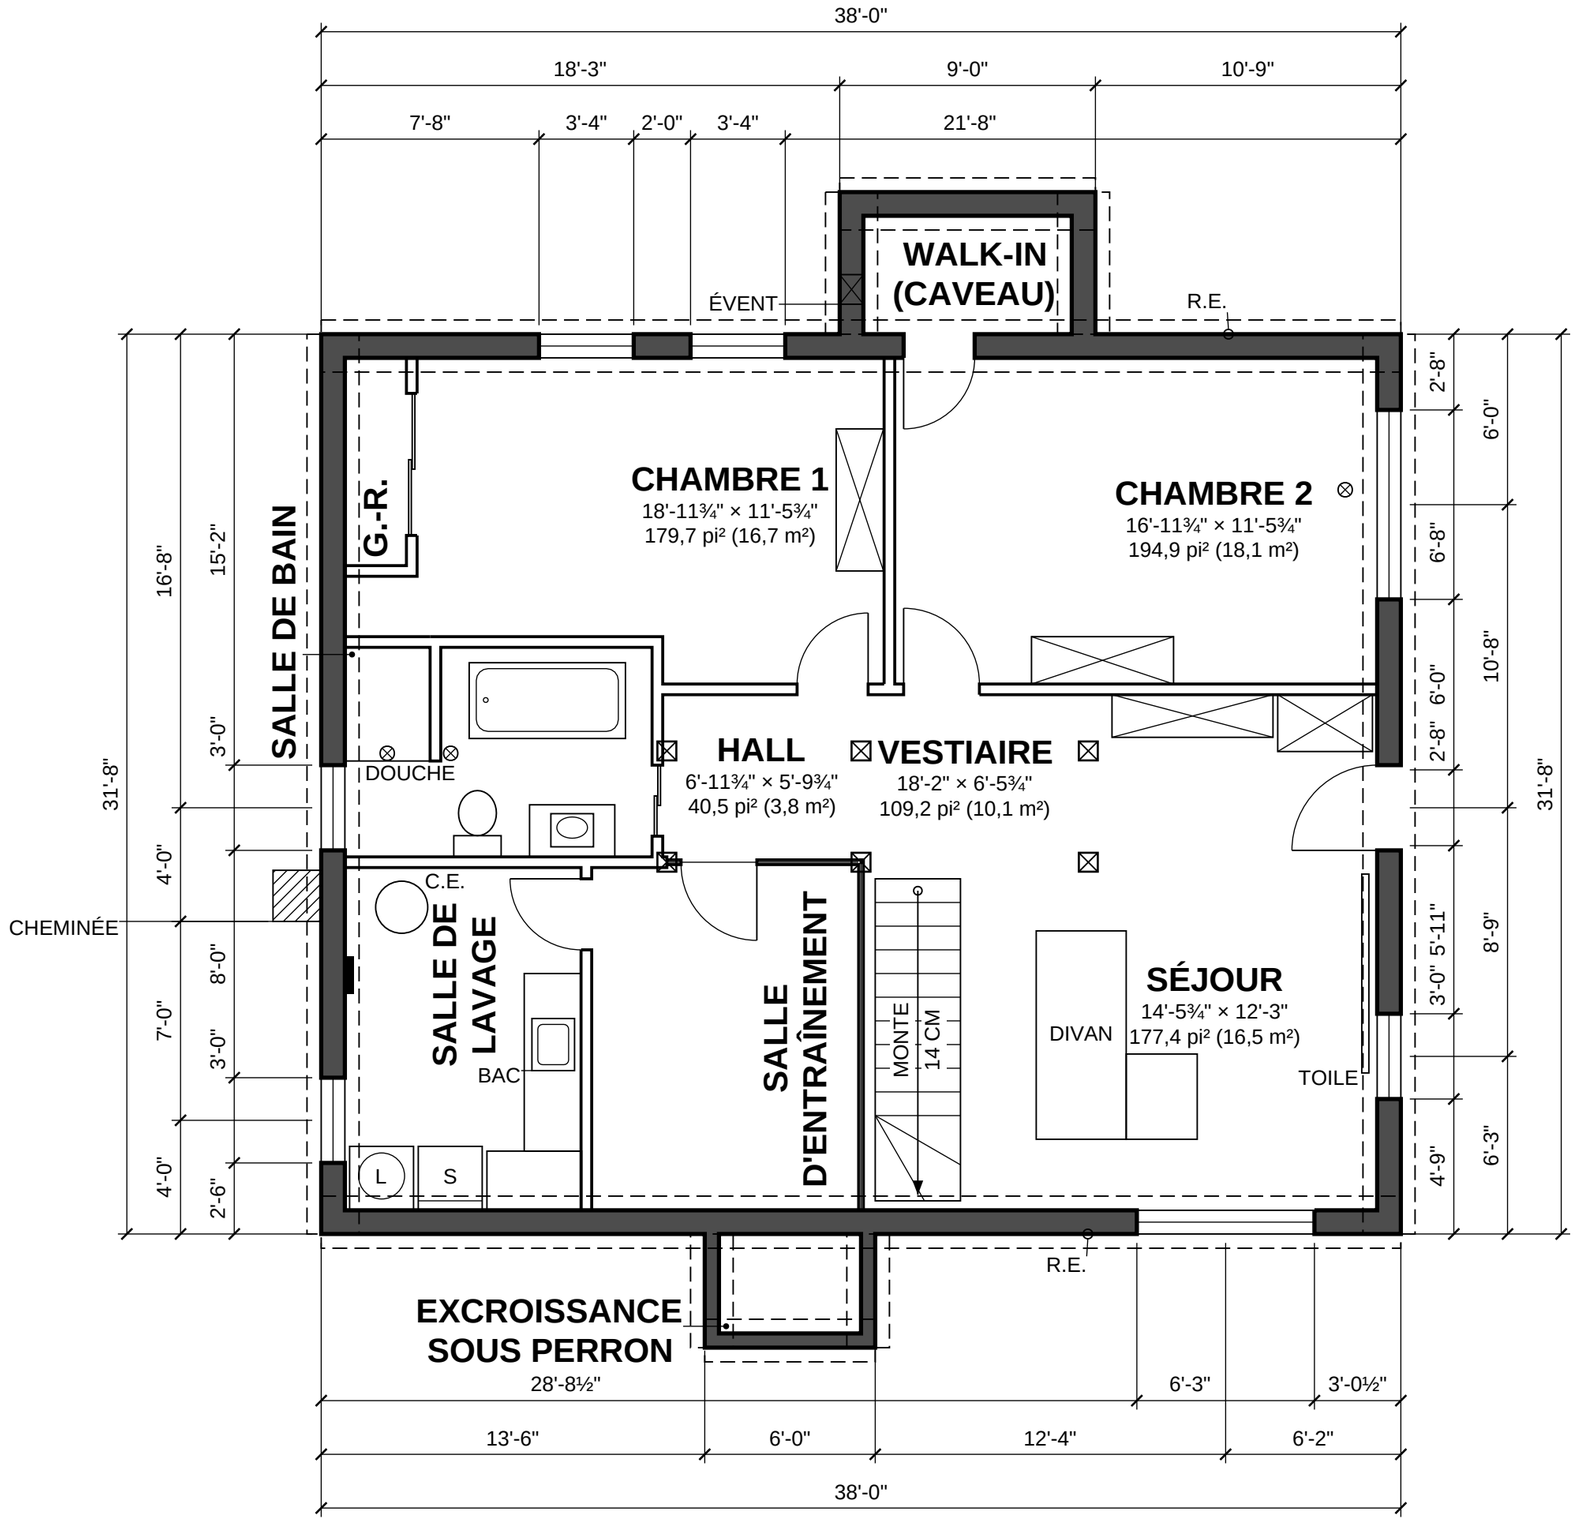


FAÇADE AVANT (RUE)

PROJET

Résidence — 86, avenue Laurier, Baie-Comeau

PROPOSITION SS-16 — LE BAIN EN VEDETTE, DOUCHE SIMPLE, BÉTON POLI — ESQUISSE À VALIDER

LÉGENDE

- Mur extérieur / fondation
- Mur intérieur existant
- Cloison projetée (nouvelle)
- Cloison vitrée projetée
- ⊠ Colonne
- ≈ Valeur estimée (mesurée sur l'image)
- ⚠n Voir registre des écarts dans RAPPORT.md
- Cotes en pieds-pouces
- ⊗ Drain
- ▬ Panneau électrique
- Petites pièces : nom seul ; dimensions et superficie dans tableau_pieces.csv

NOTES DE LA PROPOSITION

1. Esquisse : cloisons, portes, escalier, bar et appareils projetés ; le reste est l'existant (base R0).
2. Escalier de 14 c.m. à l'entrée avant (voir P-126) : trémie, giron et échappée à valider.
3. Plancher : béton poli d'un seul tenant dans tout le sous-sol (dalle meulée ou chape polie).
4. Salle de bain : bain centré sur le mur d'accent, douche simple 36 × 48 ; drains à déplacer.
5. Walk-in dans la chambre 2 ; séjour : divan en L, projecteur à côté du divan, toile.
6. Hauteur du sous-sol : 8 pi (propriétaire) ; hauteur sous poutres et coupe-feu à valider.

NORD
9,8° (sens horaire depuis +y).
Source : ESTIMÉ (P7)

ÉCHELLE GRAPHIQUE (pi)


0 — 4 — 8 — 12 pi

PHOTOS SOURCES
P2, P3

ÉCHELLE	DATE	RÉVISION
3/16" = 1'-0"	2026-11-01	A

NIVEAU
SOUS-SOL PROPOSÉ

FEUILLE
P-125

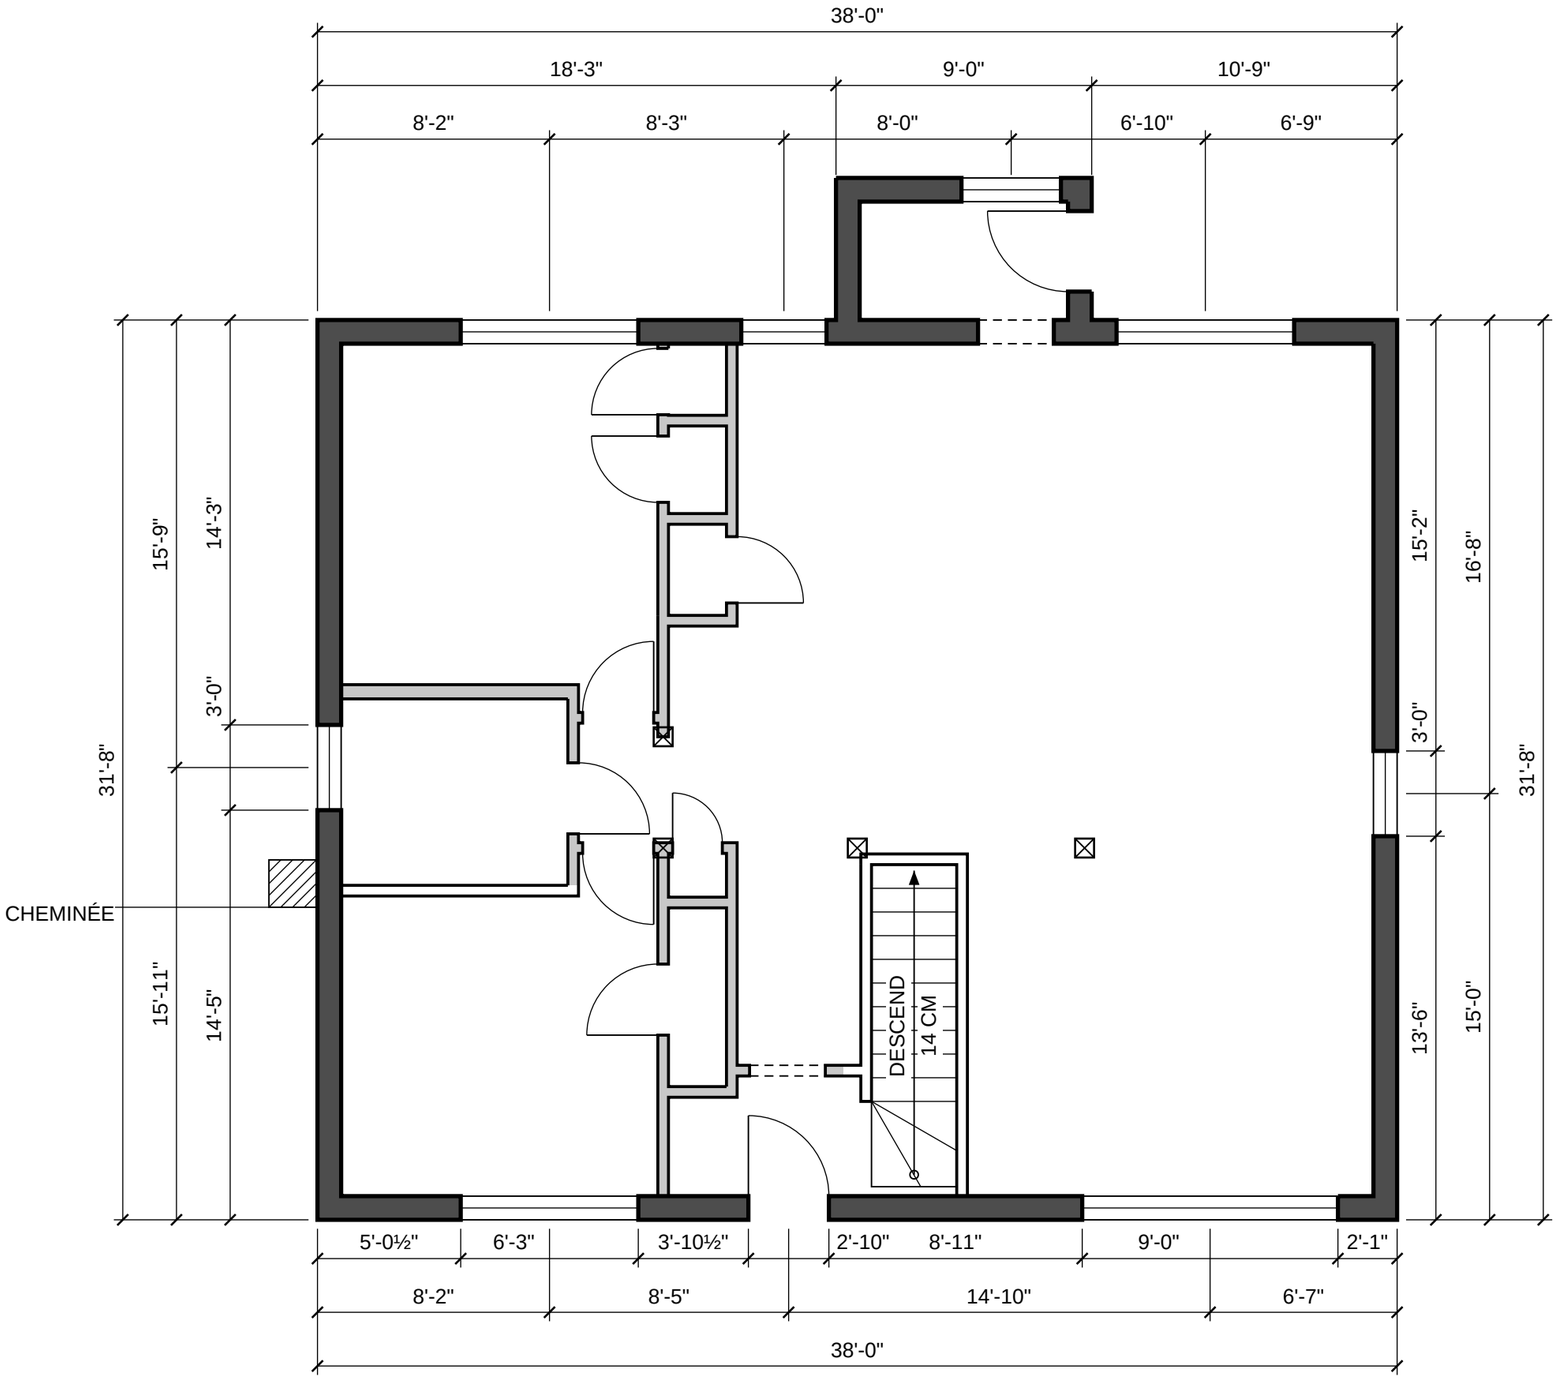

FAÇADE AVANT (RUE)

PROJET

Résidence — 86, avenue Laurier, Baie-Comeau

PROPOSITION SS-16 — LE BAIN EN VEDETTE, DOUCHE SIMPLE, BÉTON POLI — ESQUISSE À VALIDER

LÉGENDE

- Mur extérieur / fondation
- Mur intérieur existant
- Cloison projetée (nouvelle)
- ⊠ Colonne
- ≈ Valeur estimée (mesurée sur l'image)
- ⚠n Voir registre des écarts dans RAPPORT.md
- Cotes en pieds-pouces

NOTES DE LA PROPOSITION

1. Escalier à l'entrée avant (option 2) : trémie d'environ 3 × 10 pi à ouvrir dans le plancher.
2. Vestibule d'entrée commun : on descend au sous-sol ou on entre au logement du haut.
3. Cloison entre l'entrée et le salon enlevée ; cage fermée côté salon et côté hall.
4. Porte d'entrée : pentures à gauche (sens inversé) ; coupe-feu entre logements à valider.
5. Salle de bain agrandie de 1½ pi vers la chambre avant (mur déplacé) ; plomberie à vérifier.

NORD
9,8° (sens horaire depuis +y).
Source : ESTIMÉ (P7)

ÉCHELLE GRAPHIQUE (pi)

0 — 4 — 8 — 12 pi

PHOTOS SOURCES
P4, P5, P6

ÉCHELLE	DATE	RÉVISION
3/16" = 1'-0"	2026-11-01	A

NIVEAU
RDC PROPOSÉ

FEUILLE
P-126