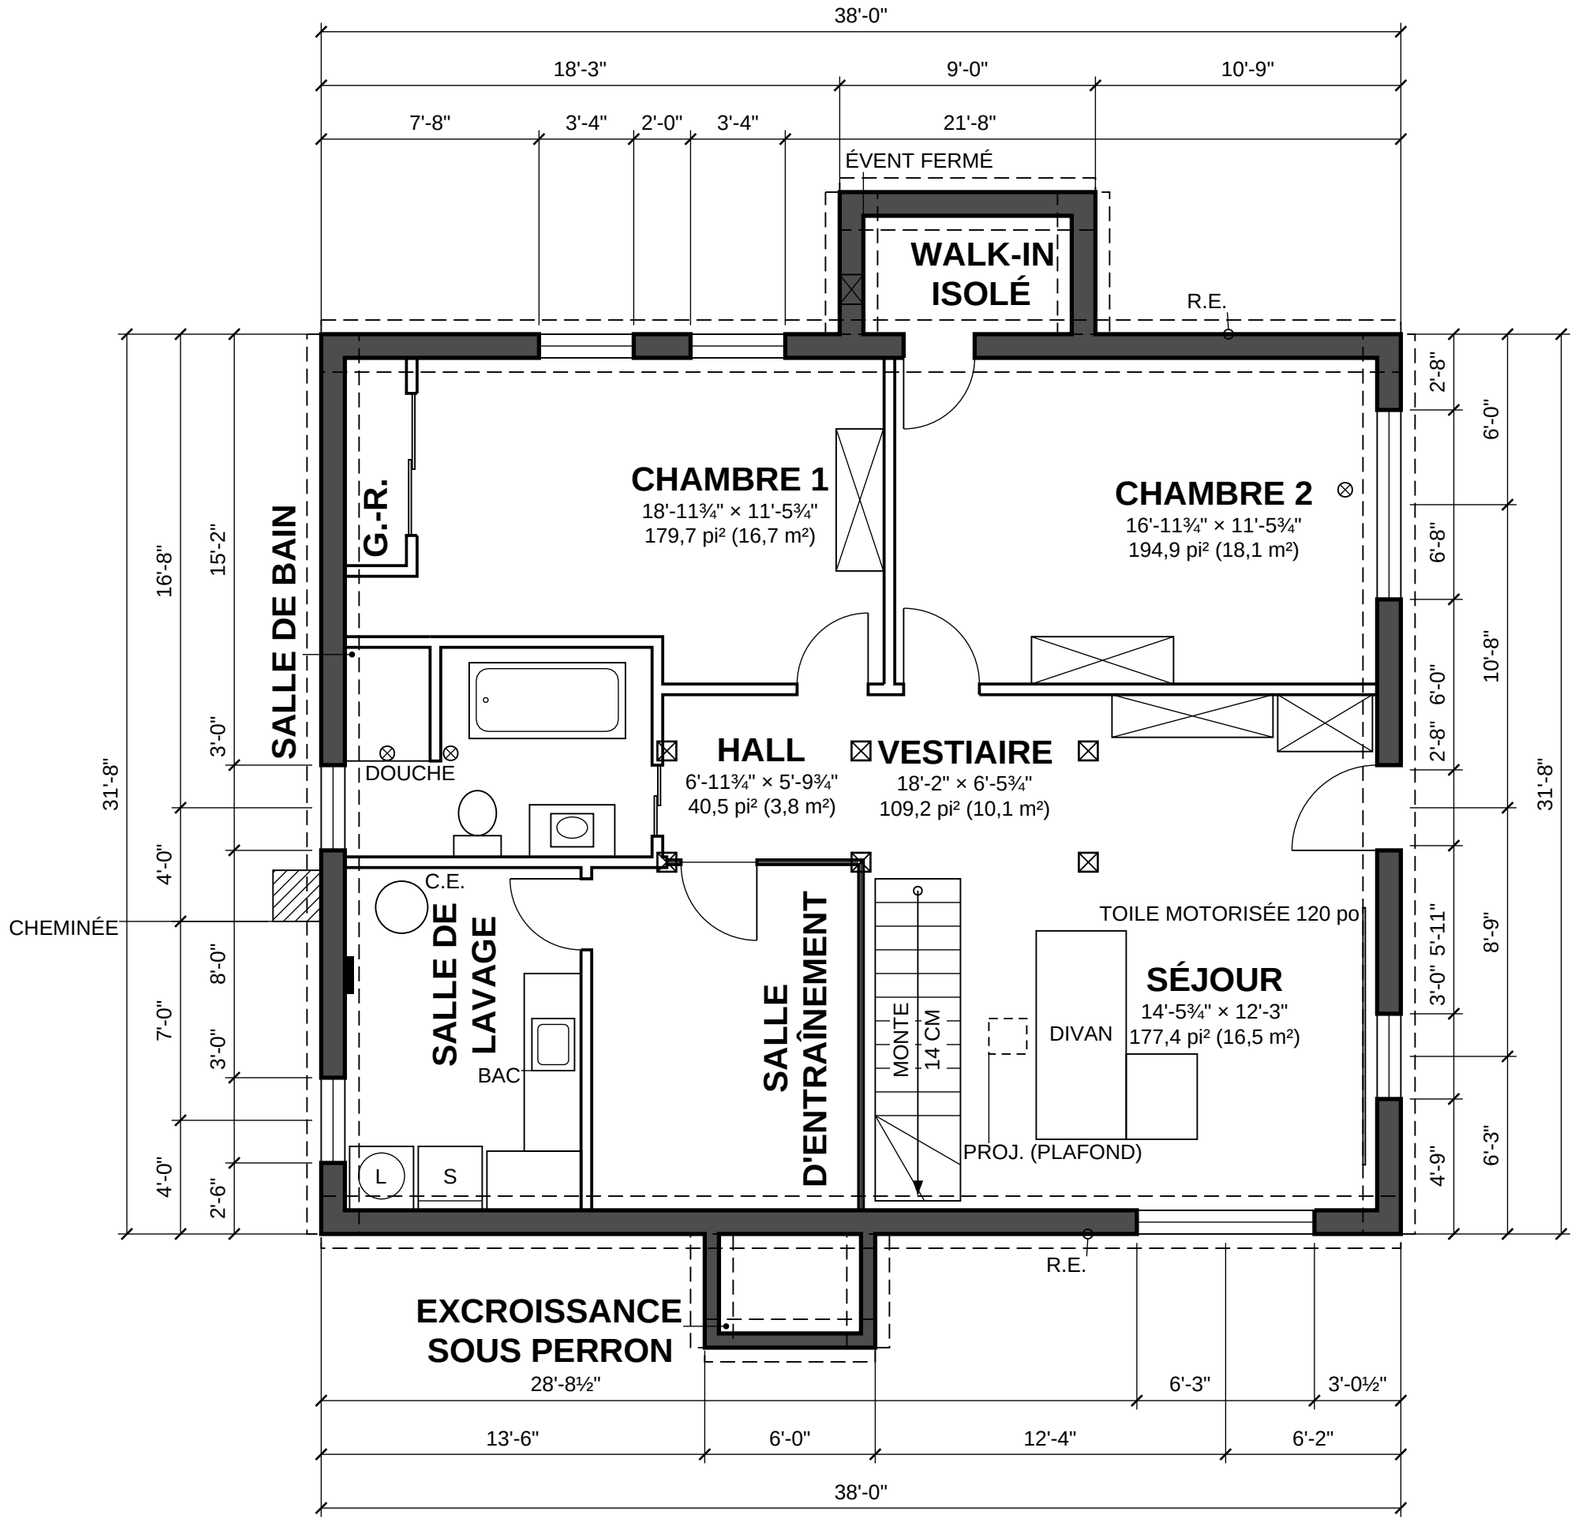


FAÇADE AVANT (RUE)

PROJET

Résidence — 86, avenue Laurier, Baie-Comeau

PROPOSITION SS-17 — RANGEMENT DES CHAMBRES D'ENFANTS, ESCALIER, GYM, SOUS-SOL OPTIMISÉ — ESQUISSE À VALIDER

LÉGENDE

- Mur extérieur / fondation
- Mur intérieur existant
- Cloison projetée (nouvelle)
- Cloison vitrée projetée
- ⊠ Colonne
- ≈ Valeur estimée (mesurée sur l'image)
- ⚠n Voir registre des écarts dans RAPPORT.md
- Cotes en pieds-pouces
- ⊗ Drain
- Panneau électrique
- Petites pièces : nom seul ; dimensions et superficie dans tableau_pieces.csv

NOTES DE LA PROPOSITION

1. Esquisse (le reste est l'existant, base R0) ; béton poli d'un seul tenant dans tout le sous-sol.
2. Escalier de 14 c.m. à l'entrée avant (voir P-126) : trémie, giron et échappée à valider.
3. Salle de bain : bain centré sur le mur d'accent, douche 36 × 48 ; drains à déplacer.
4. Séjour : toile motorisée 120 po centrée, projecteur au plafond (pointillé) ; dessous de l'escalier dégagé.
5. Walk-in (ancien caveau) : isolé, évents fermés, chauffé.
6. Hauteur : 8 pi (propriétaire) ; sous les poutres et coupe-feu à valider.

NORD

N

9,8° (sens horaire depuis +y).
Source : ESTIMÉ (P7)

ÉCHELLE GRAPHIQUE (pi)

0 4 8 12 pi

PHOTOS SOURCES

P2, P3


ÉCHELLE	DATE	RÉVISION
3/16" = 1'-0"	2026-11-01	A

NIVEAU

SOUS-SOL PROPOSÉ

FEUILLE

P-127

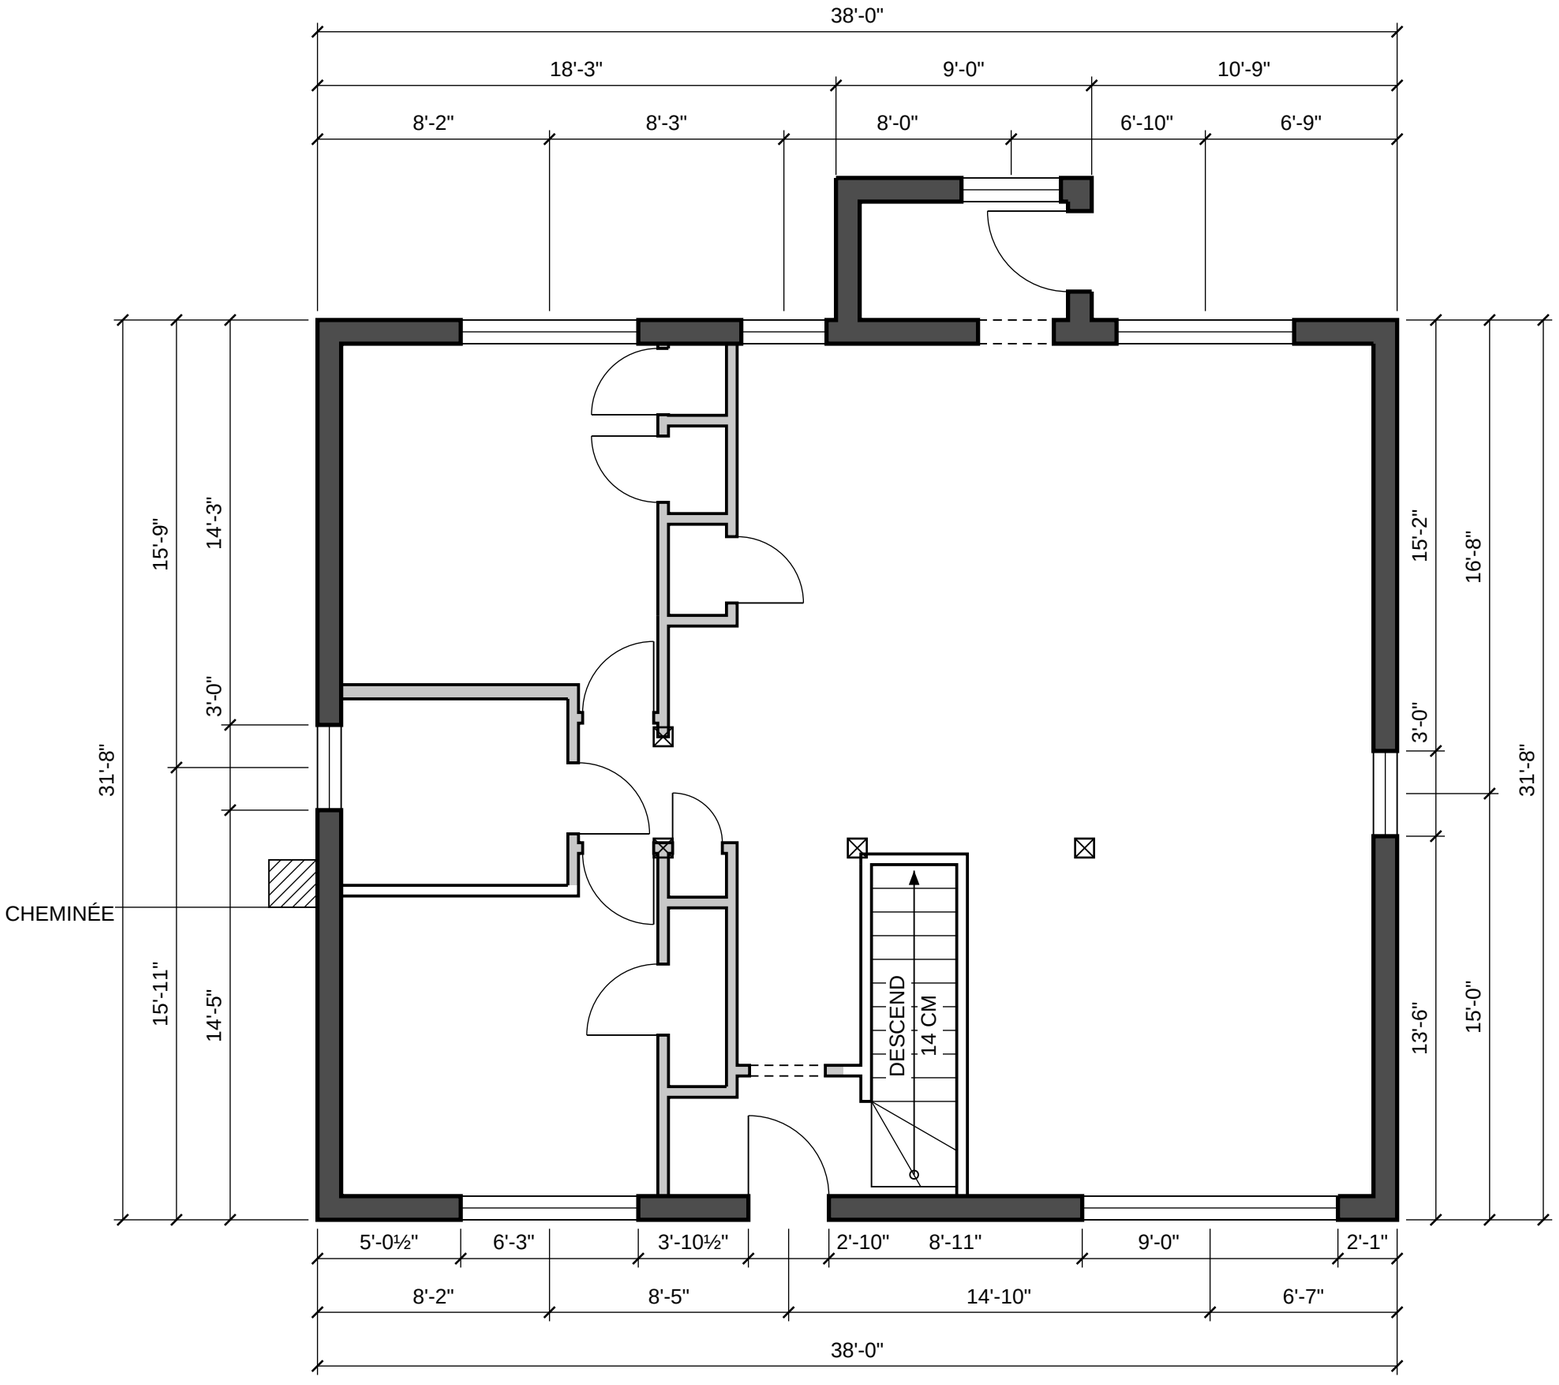

FAÇADE AVANT (RUE)

PROJET

Résidence — 86, avenue Laurier, Baie-Comeau

PROPOSITION SS-17 — RANGEMENT DES CHAMBRES D'ENFANTS, ESCALIER, GYM, SOUS-SOL OPTIMISÉ — ESQUISSE À VALIDER

LÉGENDE

- Mur extérieur / fondation
- Mur intérieur existant
- Cloison projetée (nouvelle)
- ⊠ Colonne
- ≈ Valeur estimée (mesurée sur l'image)
- ⚠n Voir registre des écarts dans RAPPORT.md
- Cotes en pieds-pouces

NOTES DE LA PROPOSITION

1. Escalier à l'entrée avant (option 2) : trémie d'environ 3 × 10 pi à ouvrir dans le plancher.
2. Vestibule d'entrée commun : on descend au sous-sol ou on entre au logement du haut.
3. Cloison entre l'entrée et le salon enlevée ; cage fermée côté salon et côté hall.
4. Porte d'entrée : pentures à gauche (sens inversé) ; coupe-feu entre logements à valider.
5. Salle de bain agrandie de 1½ pi vers la chambre avant (mur déplacé) ; plomberie à vérifier.

NORD

9,8° (sens horaire depuis +y).
Source : ESTIMÉ (P7)

ÉCHELLE GRAPHIQUE (pi)

0 — 4 — 8 — 12 pi

PHOTOS SOURCES

P4, P5, P6

ÉCHELLE	DATE	RÉVISION
3/16" = 1'-0"	2026-11-01	A

NIVEAU

RDC PROPOSÉ

FEUILLE

P-128