

Résidence — 86, avenue Laurier, Baie-Comeau — plan final MAISON-18

Révision B, 2026-11-08 · en haut : Rez-de-chaussée proposé (P-130) · en bas : Sous-sol proposé (P-129)

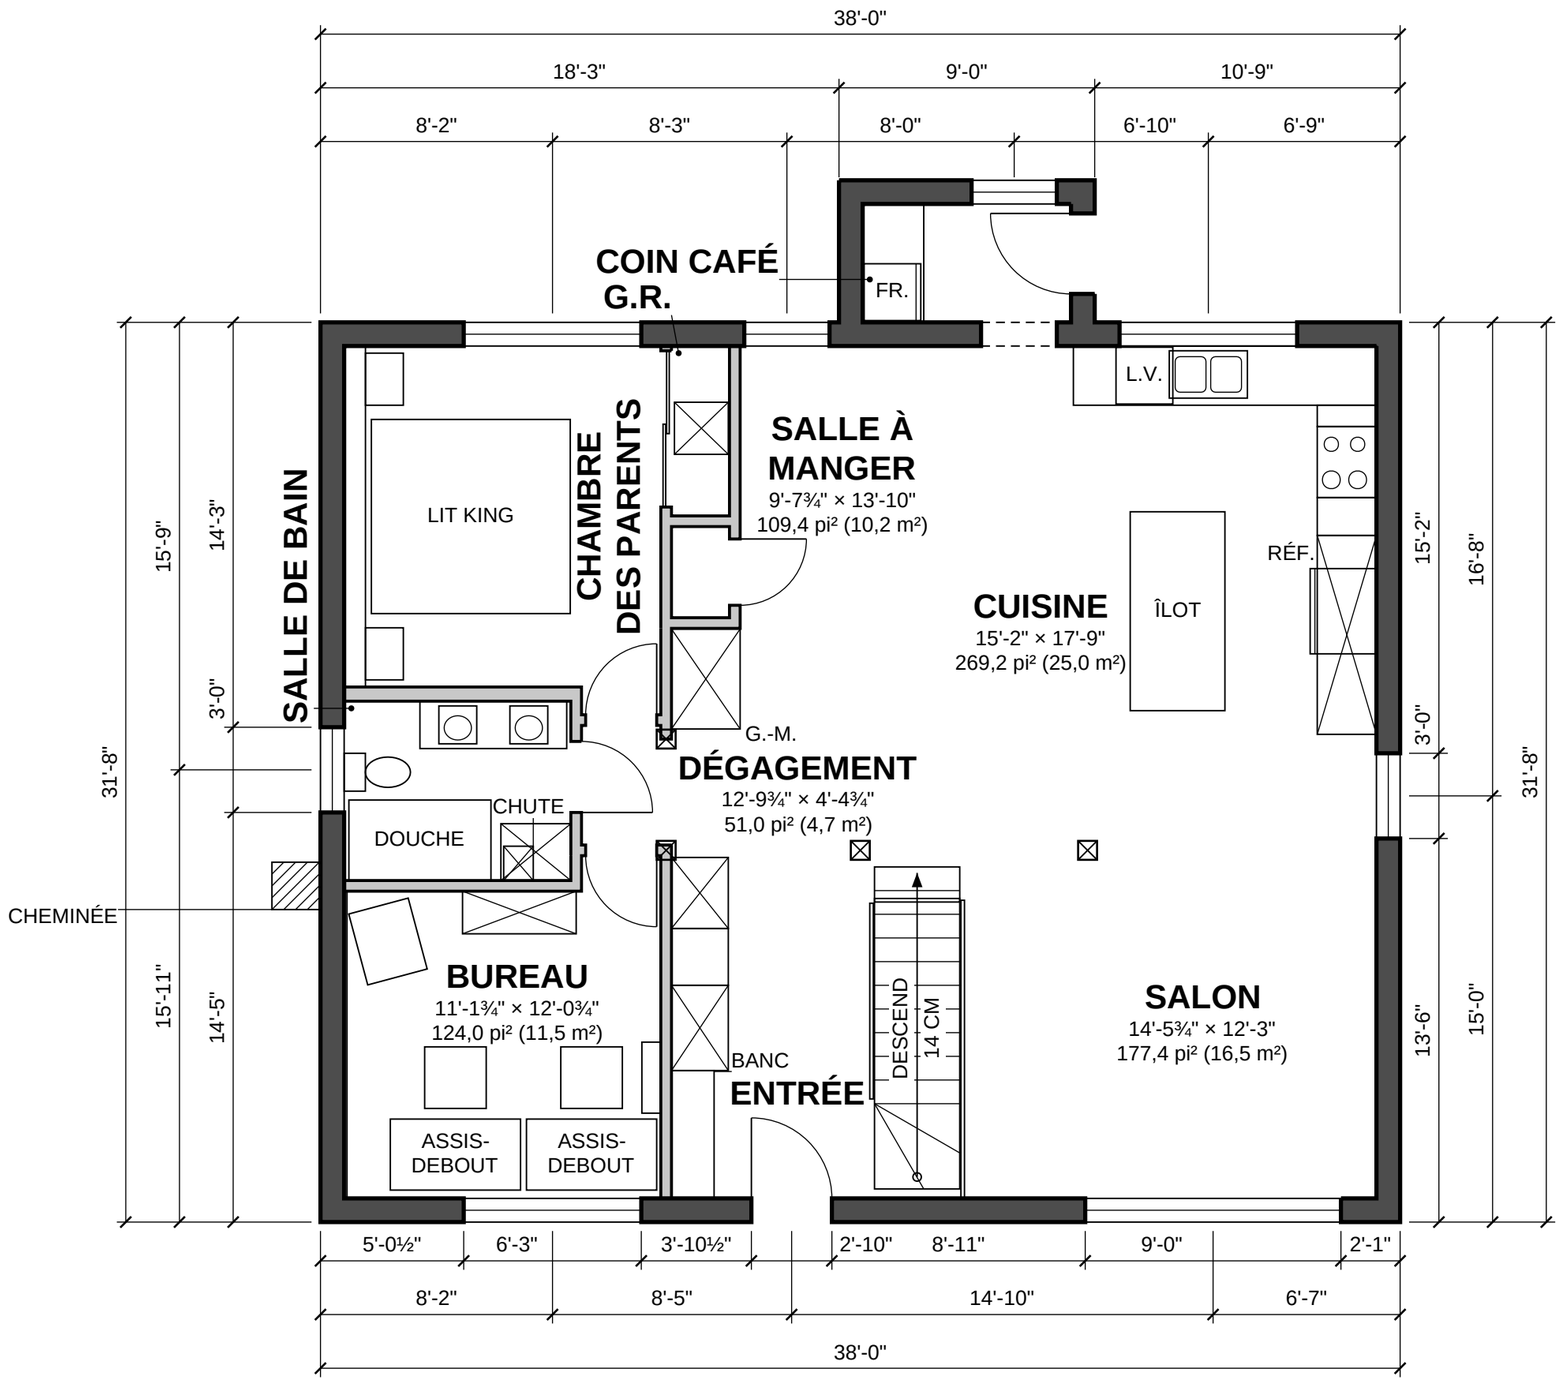

FAÇADE AVANT (RUE)

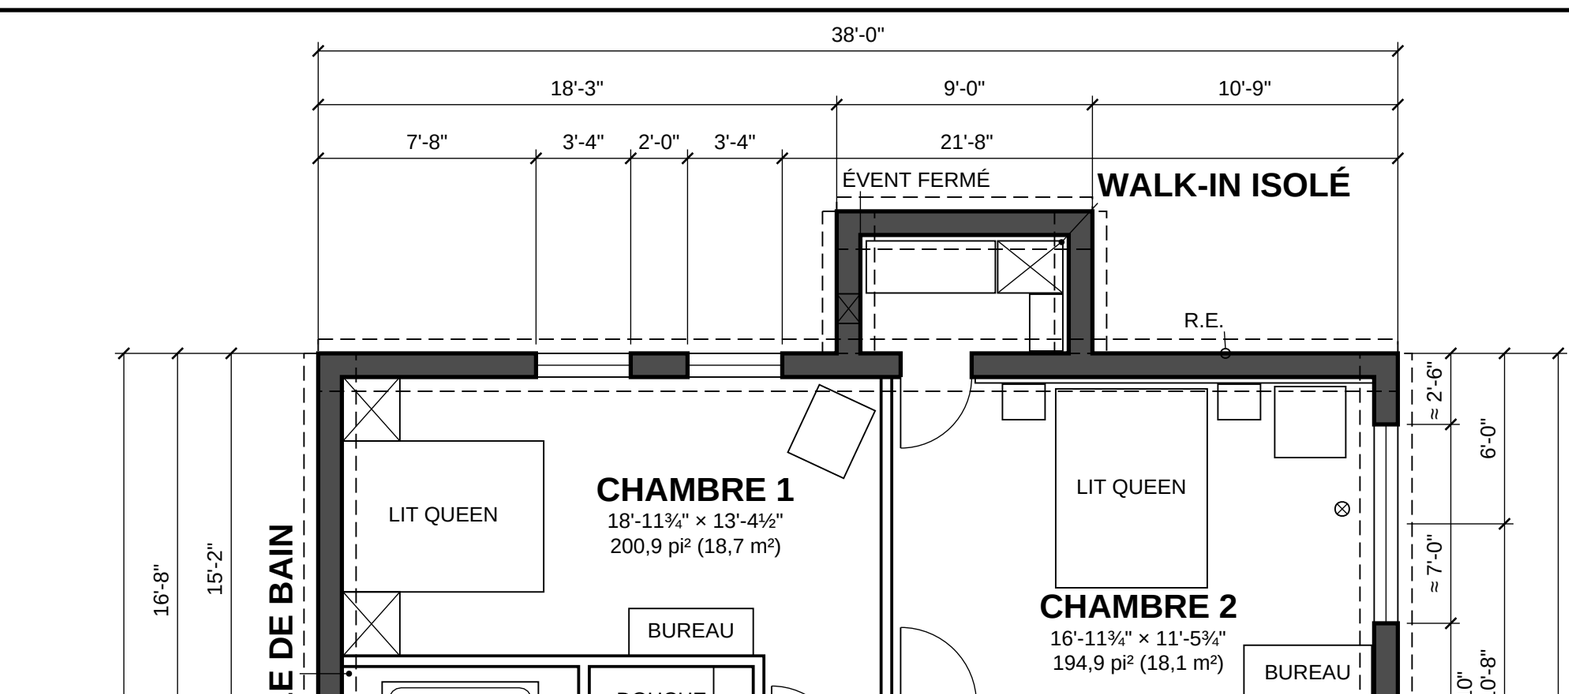

FAÇADE AVANT (RUE)

PROJET
Résidence — 86, avenue Laurier, Baie-Comeau

PLAN FINAL MAISON-18 — LES DEUX ÉTAGES : GRANDE ENTRÉE VITRÉE, CHAMBRE KING, BUREAU ASSIS-DEBOUT

LÉGENDE

- Mur extérieur / fondation
- Mur intérieur (cloison)
- Mur intérieur existant
- Cloison projetée (nouvelle)
- Cloison vitrée projetée
- Colonne
- ≈ Valeur estimée (mesurée sur l'image)
- ⚠n Voir registre des écarts dans RAPPORT.md
- Cotes en pieds-pouces
- Drain
- Panneau électrique
- Petites pièces : nom seul ; dimensions et superficie dans tableau_pieces.csv

NOTES DE LA PROPOSITION

1. Esquisse sur le relevé photo RDC-01 (le reste est l'existant ; cotes à mesurer) ; fenêtres selon la vidéo DAG (salon : allège ≈ 12 po).
2. Grande entrée ouverte : garde-robes du hall enlevées ; escalier entouré d'un garde-corps de verre.
3. Escalier vers le sous-sol : trémie ≈ 3 × 10 pi ; échappée ≈ 1,96 m à vérifier ; garde-corps de 42 po conseillé.
4. Chambre des parents : lit king, mur de tête en bois de grange, garde-robes réunies à portes coulissantes.
5. Bureau (ancienne chambre avant) : 2 bureaux assis-debout en chêne blanc face à la fenêtre avant.
6. Poutre et appuis de l'ancienne cloison hall/salon, coupe-feu entre logements : à valider avec la Ville et un professionnel.

NORD
9,8° (sens horaire depuis +y).
Source : ESTIMÉ (P7)

ÉCHELLE GRAPHIQUE (pi)
0 4 8 12 pi

PHOTOS SOURCES
photos 01 à 15 du 2026-11-01

ÉCHELLE	DATE	RÉVISION
3/16" = 1'-0"	2026-11-08	B

NIVEAU REZ-DE-CHAUSSÉE PROPOSÉ — **FEUILLE** P-130

PROJET
Résidence — 86, avenue Laurier, Baie-Comeau

PLAN FINAL MAISON-18 — LES DEUX ÉTAGES : GRANDE ENTRÉE VITRÉE, CHAMBRE KING, BUREAU ASSIS-DEBOUT

LÉGENDE

- Mur extérieur / fondation
- Mur intérieur existant
- Cloison projetée (nouvelle)
- Cloison vitrée projetée
- Colonne
- ≈ Valeur estimée (mesurée sur l'image)
- ⚠n Voir registre des écarts dans RAPPORT.md
- Cotes en pieds-pouces
- Drain
- Panneau électrique
- Petites pièces : nom seul ; dimensions et superficie dans tableau_pieces.csv

NOTES DE LA PROPOSITION

1. Fenêtres selon la vidéo DAG (allège ≈ 44, tête ≈ 80 po ; chambre 1 : allège ≈ 40) ; congélateur au lavage.
2. Chute à linge (salle de bain du haut → plafond du lavage) : déflecteur inox, chariot ; cloison, solives et coupe-feu à valider.
3. Hall : mur épais sous la poutre arrière (colonnes cachées) ; chambre 1 et salle de bain agrandies ; fenêtres d'évacuation à vérifier.
4. Walk-in (ancien caveau) : isolé, évents fermés, chauffé ; porte dérobée dans le mur de chêne de la chambre 2.

… autres notes : voir maison.json

NORD
9,8° (sens horaire depuis +y).
Source : ESTIMÉ (P7)

ÉCHELLE GRAPHIQUE (pi)
0 4 8 12 pi

PHOTOS SOURCES
P2, P3

ÉCHELLE	DATE	RÉVISION
3/16" = 1'-0"	2026-11-08	B

NIVEAU SOUS-SOL PROPOSÉ — **FEUILLE** P-129

Visite 3D de la maison

https://claude.ai/artifact/BcvbdKVk2VjTxMswm2JYLC

Touchez le lien ou balayez le code avec le téléphone pour faire la visite.

Lien privé : il s'ouvre avec le compte du propriétaire ; pour le donner à quelqu'un, le partager d'abord (menu Partager de la page).

Feuilles à l'échelle 3/16" = 1'-0" sur 11 × 17 : imprimer MAISON-18_deux_etages.pdf. Sur cette page assemblée, se fier à l'échelle graphique de chaque feuille.