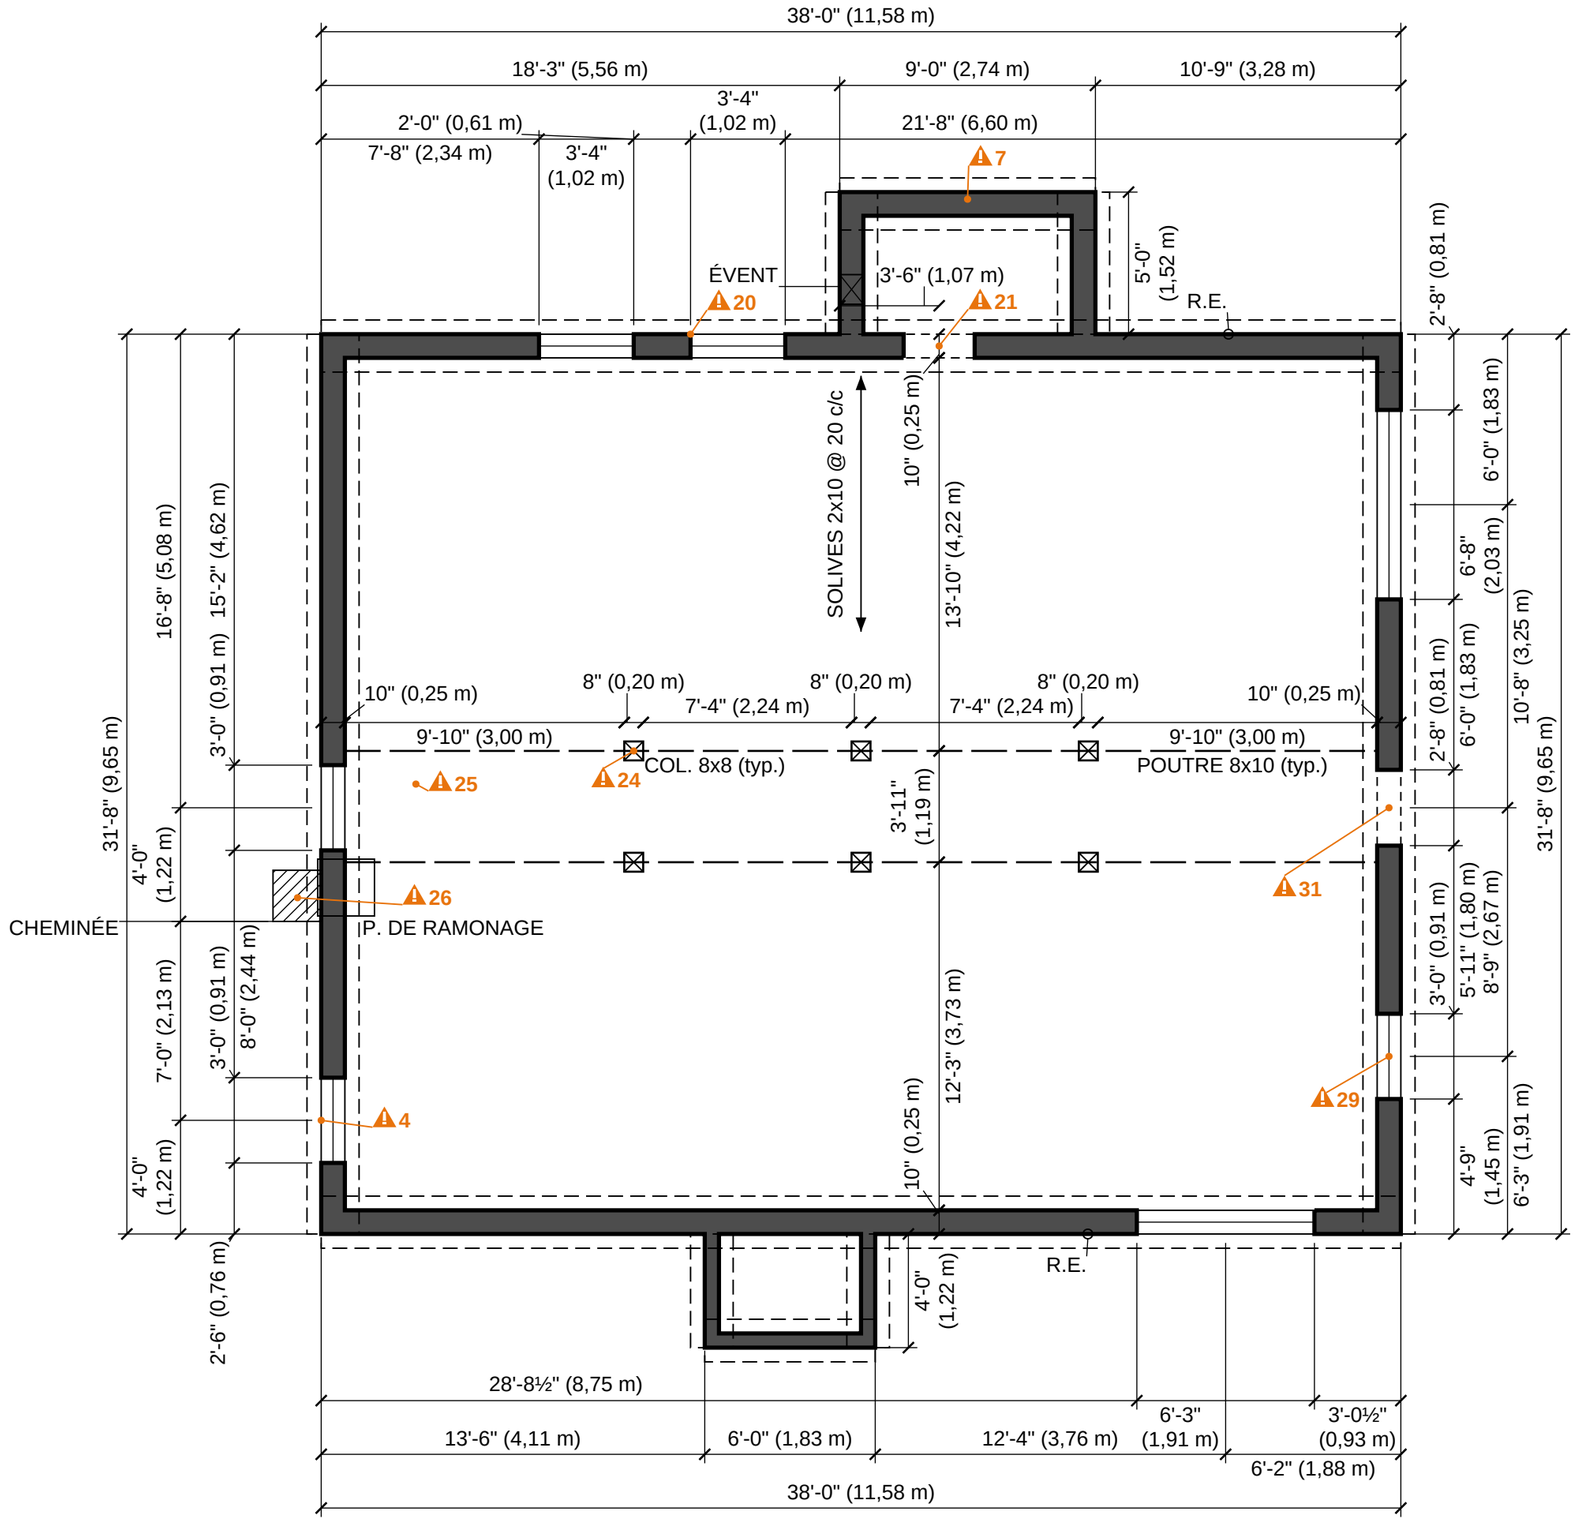


FAÇADE AVANT (RUE)

PROJET

Résidence — 86, avenue Laurier, Baie-Comeau

RELEVÉ DE L'EXISTANT — PRÉLIMINAIRE, À VALIDER SUR PLACE

LÉGENDE

- Mur extérieur / fondation
- Mur intérieur (cloison)
- Poutre (au-dessus)
- Axe porteur d'origine
- Colonne
- Solives (sens)
- ≈ Valeur estimée (mesurée sur l'image)
- ⚠n Voir registre des écarts dans RAPPORT.md
- Cotes en pi-po (métrique en m) (typ.) : libellé typique, vaut pour les éléments identiques
- Noms, dimensions et superficies des pièces : voir tableau_pieces.csv

REPÈRES SUR CETTE FEUILLE

- ⚠4 Cote en conflit cote-SS-017 — Largeur de la fenêtre gauche basse du sous-sol (au-dessus de l'évier à lessive). Lecture … [ecart-004 — voir RAPPORT.md]
- ⚠7 Tous les murs sans cote d'épaisseur : 10", 6" présumé (4 murs, repère unique). Épaisseurs PRÉSUMÉES par analogie … [ecart-007 — voir RAPPORT.md]
- ⚠20 Fenêtres arrière et droite haute du sous-sol : « 6'-8" » confirmé par la 3e lecture, mais dessinées de la même … [ecart-020 — voir RAPPORT.md]

… liste complète : donnees/verifications.txt

NORD
9,8° (sens horaire depuis +y).
Source : ESTIMÉ (P7)

ÉCHELLE GRAPHIQUE (pi)


0 — 4 — 8 — 12 pi

PHOTOS SOURCES
P2, P3

ÉCHELLE	DATE	RÉVISION
3/16" = 1'-0"	2026-10-29	R0

NIVEAU
SOUS-SOL

FEUILLE
A-100

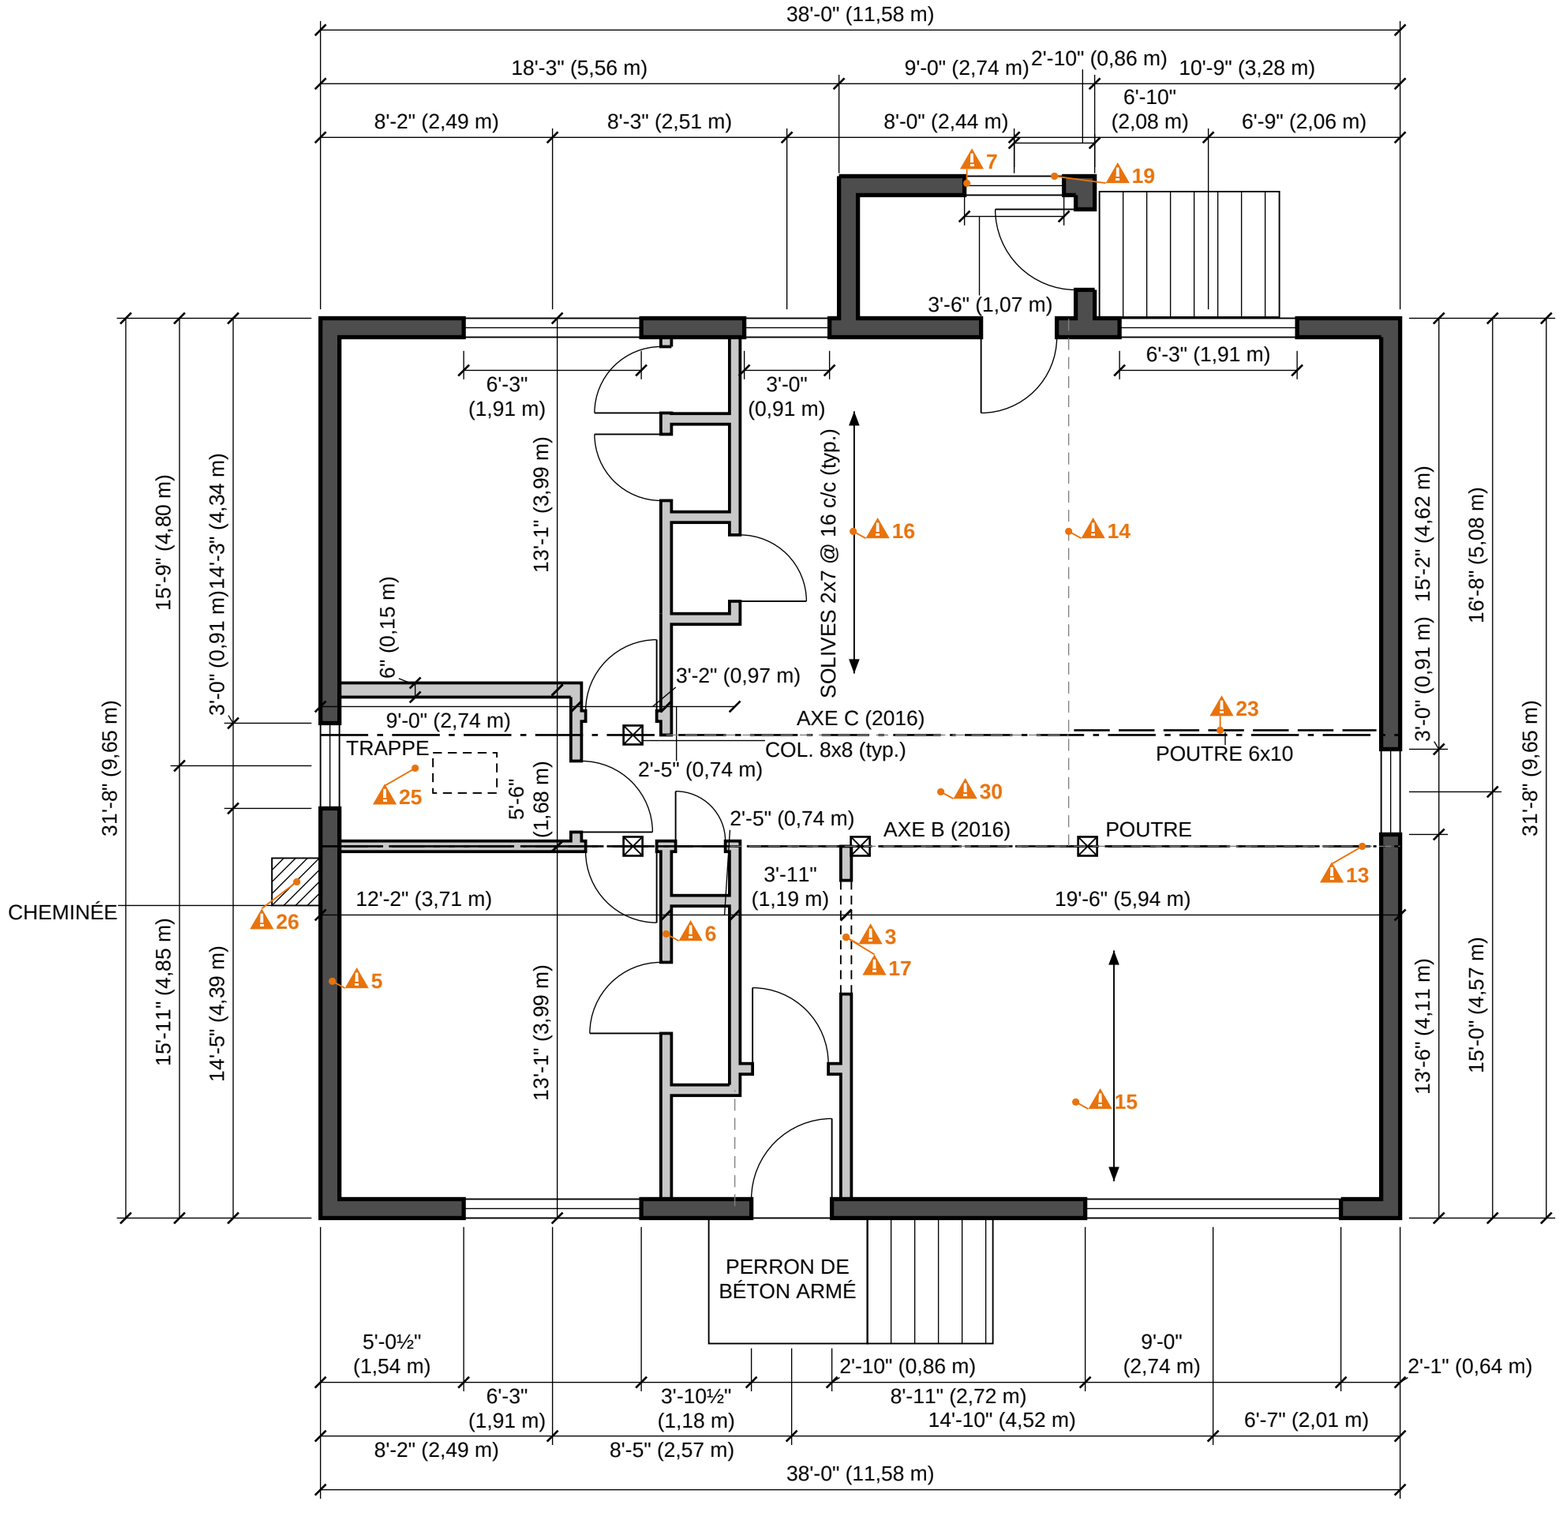

FAÇADE AVANT (RUE)

PROJET

Résidence — 86, avenue Laurier, Baie-Comeau

RELEVÉ DE L'EXISTANT — PRÉLIMINAIRE, À VALIDER SUR PLACE

LÉGENDE

- Mur extérieur / fondation
- Mur intérieur (cloison)
- Poutre (au-dessus)
- Axe porteur d'origine
- Colonne
- Solives (sens)
- ≈ Valeur estimée (mesurée sur l'image)
- ⚠n Voir registre des écarts dans RAPPORT.md
- Cotes en pi-po (métrique en m)
- Limite de zone ouverte (aucun mur)
- (typ.) : libellé typique, vaut pour les éléments identiques
- Noms, dimensions et superficies des pièces : voir tableau_pieces.csv

REPÈRES SUR CETTE FEUILLE

- ⚠3 Cote en conflit cote-RDC-048 — Largeur de l'arche hall / salon : écrit « ARCHE 4'-0" » (2 lectures) contre 6'-0" (3e lecture) … [ecart-003 — voir RAPPORT.md]
- ⚠5 Épaisseur des murs extérieurs du RDC : 10" écrit sur le croquis 2016 (P1, chaînes 10" aux 4 côtés — valeur typique d'une … [ecart-005 — voir RAPPORT.md]
- ⚠6 Toutes les cloisons sans cote d'épaisseur : 4½" présumé (14 murs, repère unique). Épaisseur des cloisons du RDC non … [ecart-006 — voir RAPPORT.md]

… liste complète : donnees/verifications.txt

NORD
9,8° (sens horaire depuis +y).
Source : ESTIMÉ (P7)

ÉCHELLE GRAPHIQUE (pi)

0 4 8 12 pi

PHOTOS SOURCES
P4, P5, P6

ÉCHELLE	DATE	RÉVISION
3/16" = 1'-0"	2026-10-29	R0

NIVEAU	FEUILLE
REZ-DE-CHAUSSÉE	A-101