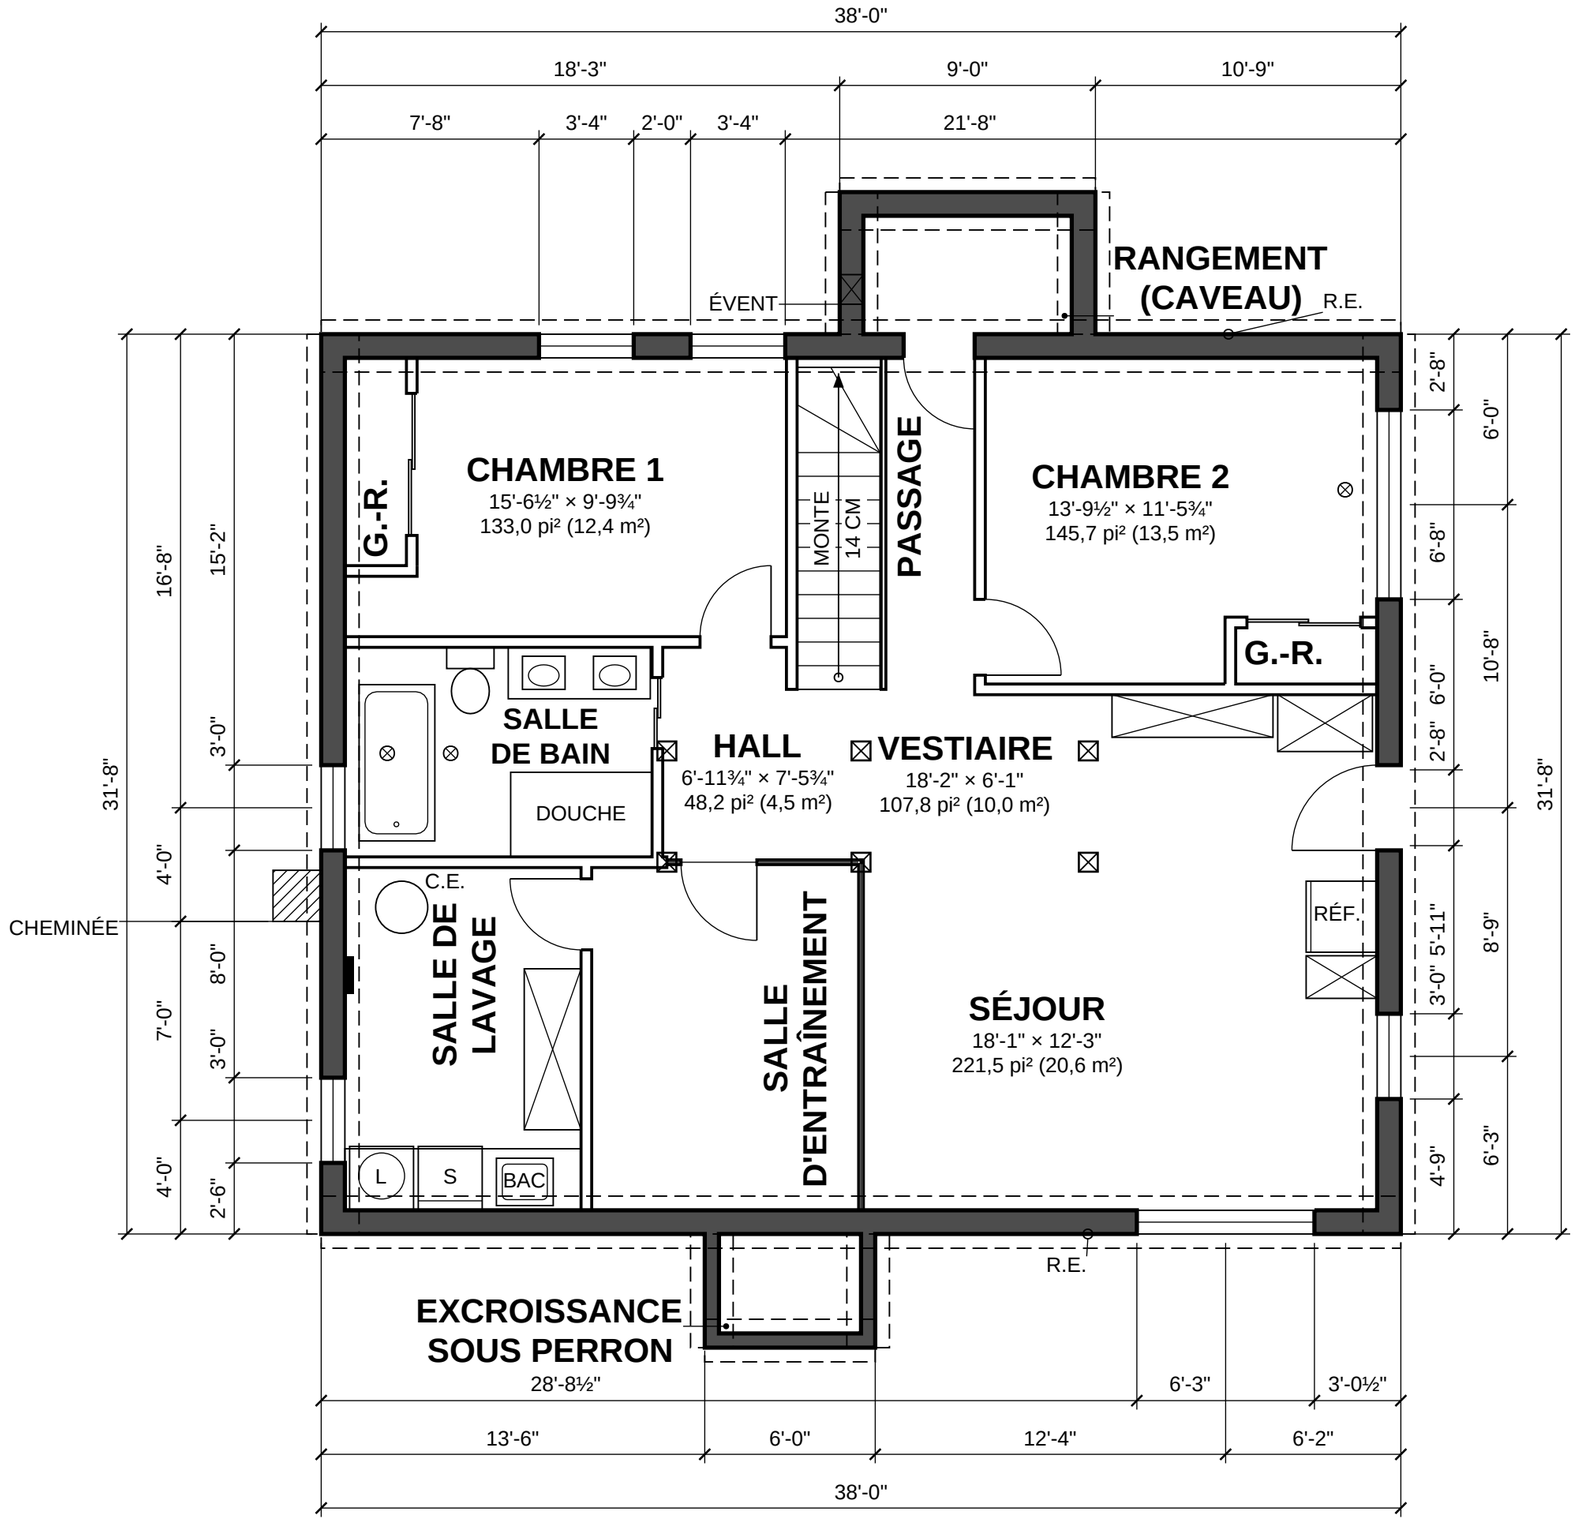


FAÇADE AVANT (RUE)

PROJET

Résidence — 86, avenue Laurier, Baie-Comeau

PROPOSITION SS-09 — ESCALIER À L'EST DE LA FENÊTRE DE LA CHAMBRE — ESQUISSE À VALIDER

LÉGENDE

- Mur extérieur / fondation
- Mur intérieur existant
- Cloison projetée (nouvelle)
- Cloison vitrée projetée
- ⊠ Colonne
- ≈ Valeur estimée (mesurée sur l'image)
- ⚠n Voir registre des écarts dans RAPPORT.md
- Cotes en pieds-pouces
- ⊗ Drain
- ▬ Panneau électrique
- Petites pièces : nom seul ; dimensions et superficie dans tableau_pieces.csv

NOTES DE LA PROPOSITION

1. Esquisse : cloisons, portes, escalier, bar et appareils projetés ; le reste est l'existant (base R0).
2. Escalier de 14 c.m. entre la fenêtre de la chambre et le caveau (voir P-112) : à valider.
3. Chambre 1 : mur déplacé à l'est de sa fenêtre arrière, fenêtre entière.
4. Salle de bain : bain autoportant et toilette déplacés, drains existants ignorés (tranchée).
5. Vestiaire près de l'entrée ; coin frigo dans le séjour (prise dédiée à prévoir).
6. Hauteur du sous-sol : 8 pi (propriétaire) ; hauteur sous poutres et coupe-feu à valider.

NORD

9,8° (sens horaire depuis +y).
Source : ESTIMÉ (P7)

ÉCHELLE GRAPHIQUE (pi)

0 — 4 — 8 — 12 pi

PHOTOS SOURCES

P2, P3


ÉCHELLE	DATE	RÉVISION
3/16" = 1'-0"	2026-10-29	A

NIVEAU

SOUS-SOL PROPOSÉ

FEUILLE

P-111

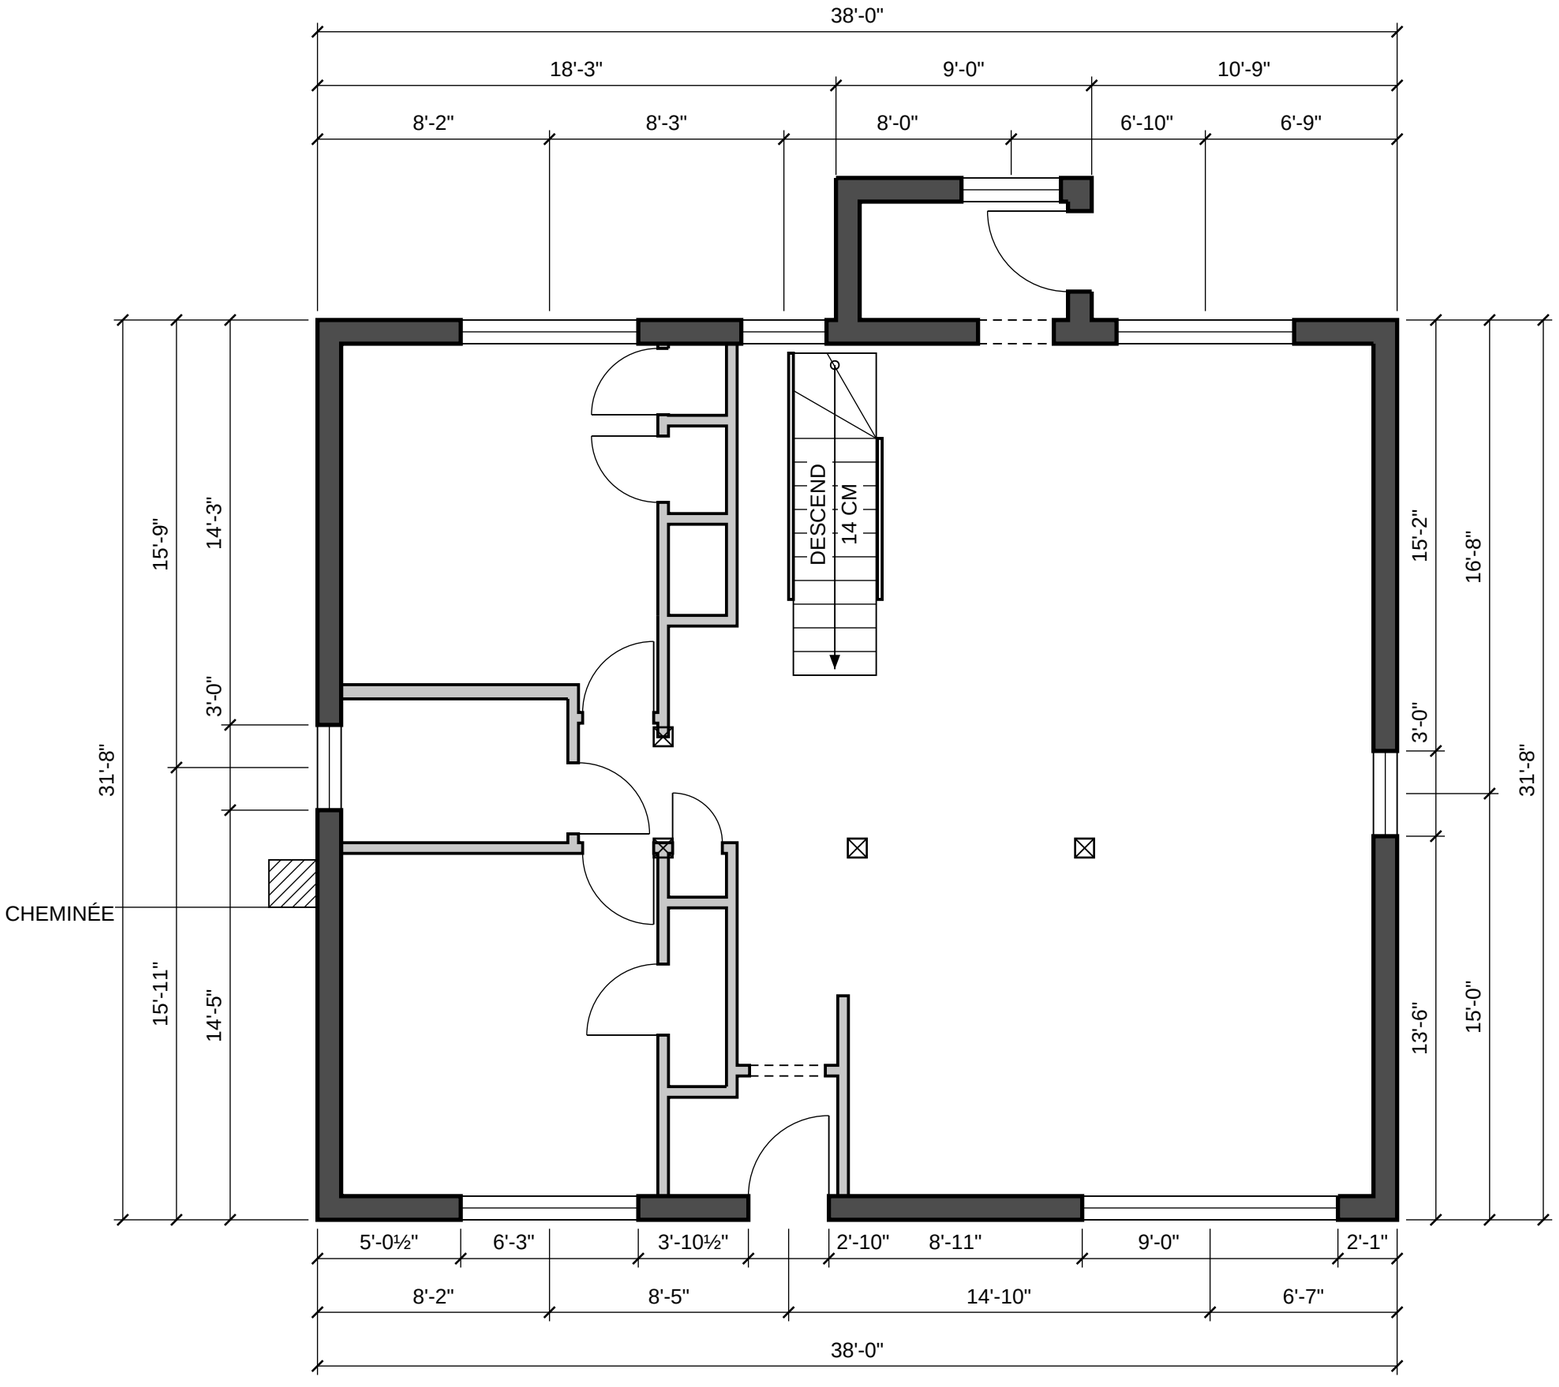

FAÇADE AVANT (RUE)

PROJET

Résidence — 86, avenue Laurier, Baie-Comeau

PROPOSITION SS-09 — ESCALIER À L'EST DE LA FENÊTRE DE LA CHAMBRE — ESQUISSE À VALIDER

LÉGENDE

- Mur extérieur / fondation
- Mur intérieur existant
- Cloison projetée (nouvelle)
- ⊠ Colonne
- ≈ Valeur estimée (mesurée sur l'image)
- ⚠n Voir registre des écarts dans RAPPORT.md
- Cotes en pieds-pouces

NOTES DE LA PROPOSITION

1. Escalier (même emplacement qu'au sous-sol) : trémie d'environ 3 × 9 pi à ouvrir.
2. Entrée par la droite, au fond (3 marches tournantes) ; gardes en lattes de chêne des deux côtés.
3. Bande libre de 2 pi entre les garde-robes et l'escalier : garde-robes plus profondes ou bibliothèque.
4. Fenêtre arrière au-dessus du haut de l'escalier ; séparation coupe-feu entre logements à valider.

NORD

9,8° (sens horaire depuis +y).
Source : ESTIMÉ (P7)

ÉCHELLE GRAPHIQUE (pi)

0 — 4 — 8 — 12 pi

PHOTOS SOURCES

P4, P5, P6

ÉCHELLE	DATE	RÉVISION
3/16" = 1'-0"	2026-10-29	A

NIVEAU

RDC PROPOSÉ

FEUILLE

P-112