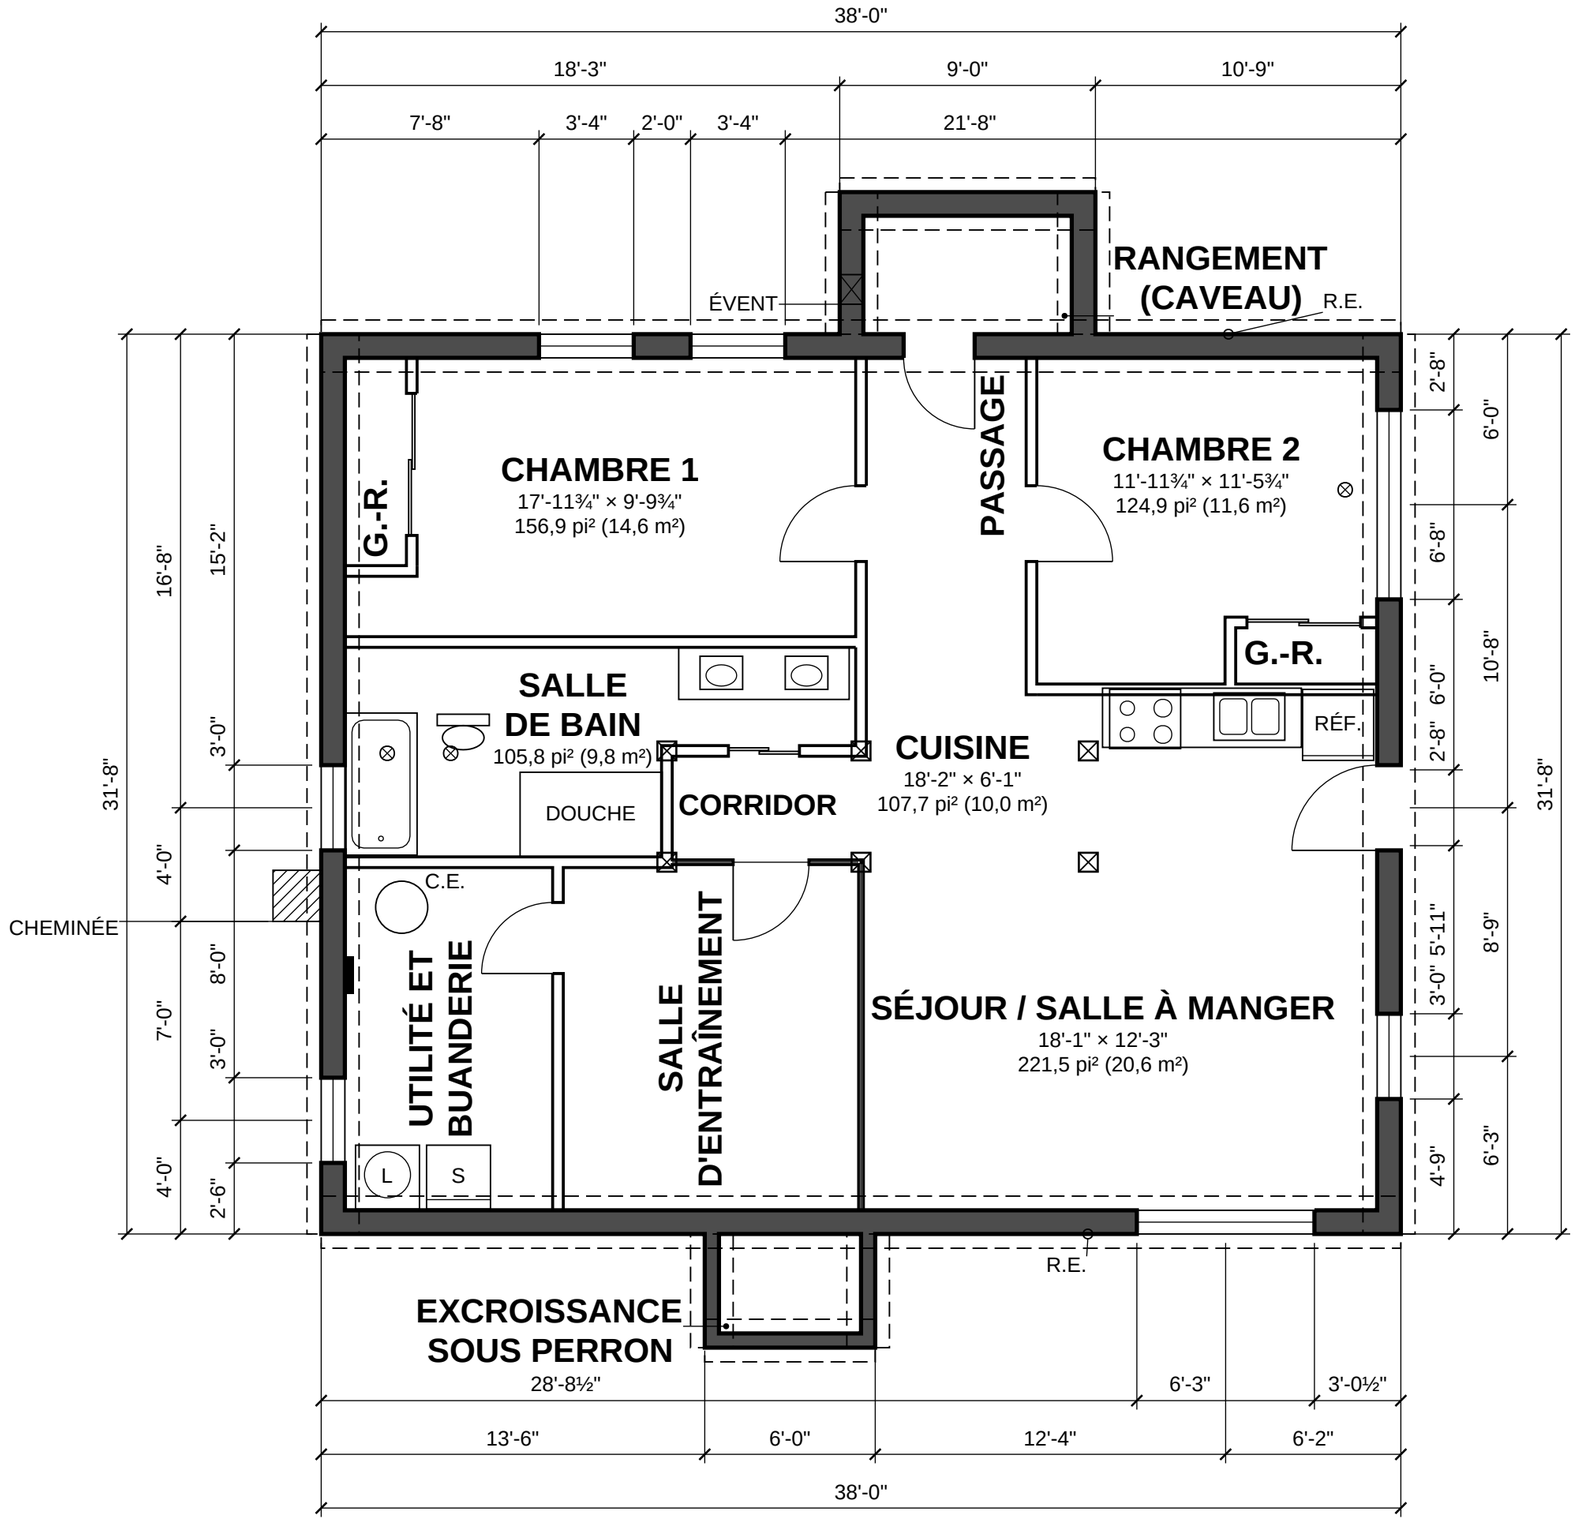

FAÇADE AVANT (RUE)

PROJET

Résidence — 86, avenue Laurier, Baie-Comeau

PROPOSITION SS-03 — GRANDE SALLE DE BAIN, CUISINE, CAVEAU EN RANGEMENT — ESQUISSE À VALIDER

LÉGENDE

- Mur extérieur / fondation
- Mur intérieur existant
- Cloison projetée (nouvelle)
- Cloison vitrée projetée
- ⊠ Colonne
- ≈ Valeur estimée (mesurée sur l'image)
- ⚠n Voir registre des écarts dans RAPPORT.md
- Cotes en pieds-pouces
- ⊗ Drain
- ▬ Panneau électrique
- Petites pièces : nom seul ; dimensions et superficie dans tableau_pieces.csv

NOTES DE LA PROPOSITION

1. Esquisse : cloisons, portes, cuisine et appareils sanitaires projetés ; le reste est l'existant (plans de base R0).
2. Salle de bain sur les drains existants (bain sous la fenêtre, toilette murale) ; vanité double dans l'alcôve, porte coulissante.
3. Évier de cuisine à environ 8 pi du drain existant : raccord sous dalle à prévoir.
4. Caveau : rangement fermé ; prévoir isolation et déshumidification avant d'y ranger des objets sensibles.
5. Fenêtres des chambres à vérifier pour l'évacuation ; hauteur sous poutres et séparation coupe-feu à valider.

NORD

N

9,8° (sens horaire depuis +y).
Source : ESTIMÉ (P7)

ÉCHELLE GRAPHIQUE (pi)

0 4 8 12 pi

PHOTOS SOURCES

P2, P3

ÉCHELLE	DATE	RÉVISION
3/16" = 1'-0"	2026-10-29	A

NIVEAU

SOUS-SOL PROPOSÉ

FEUILLE

P-102