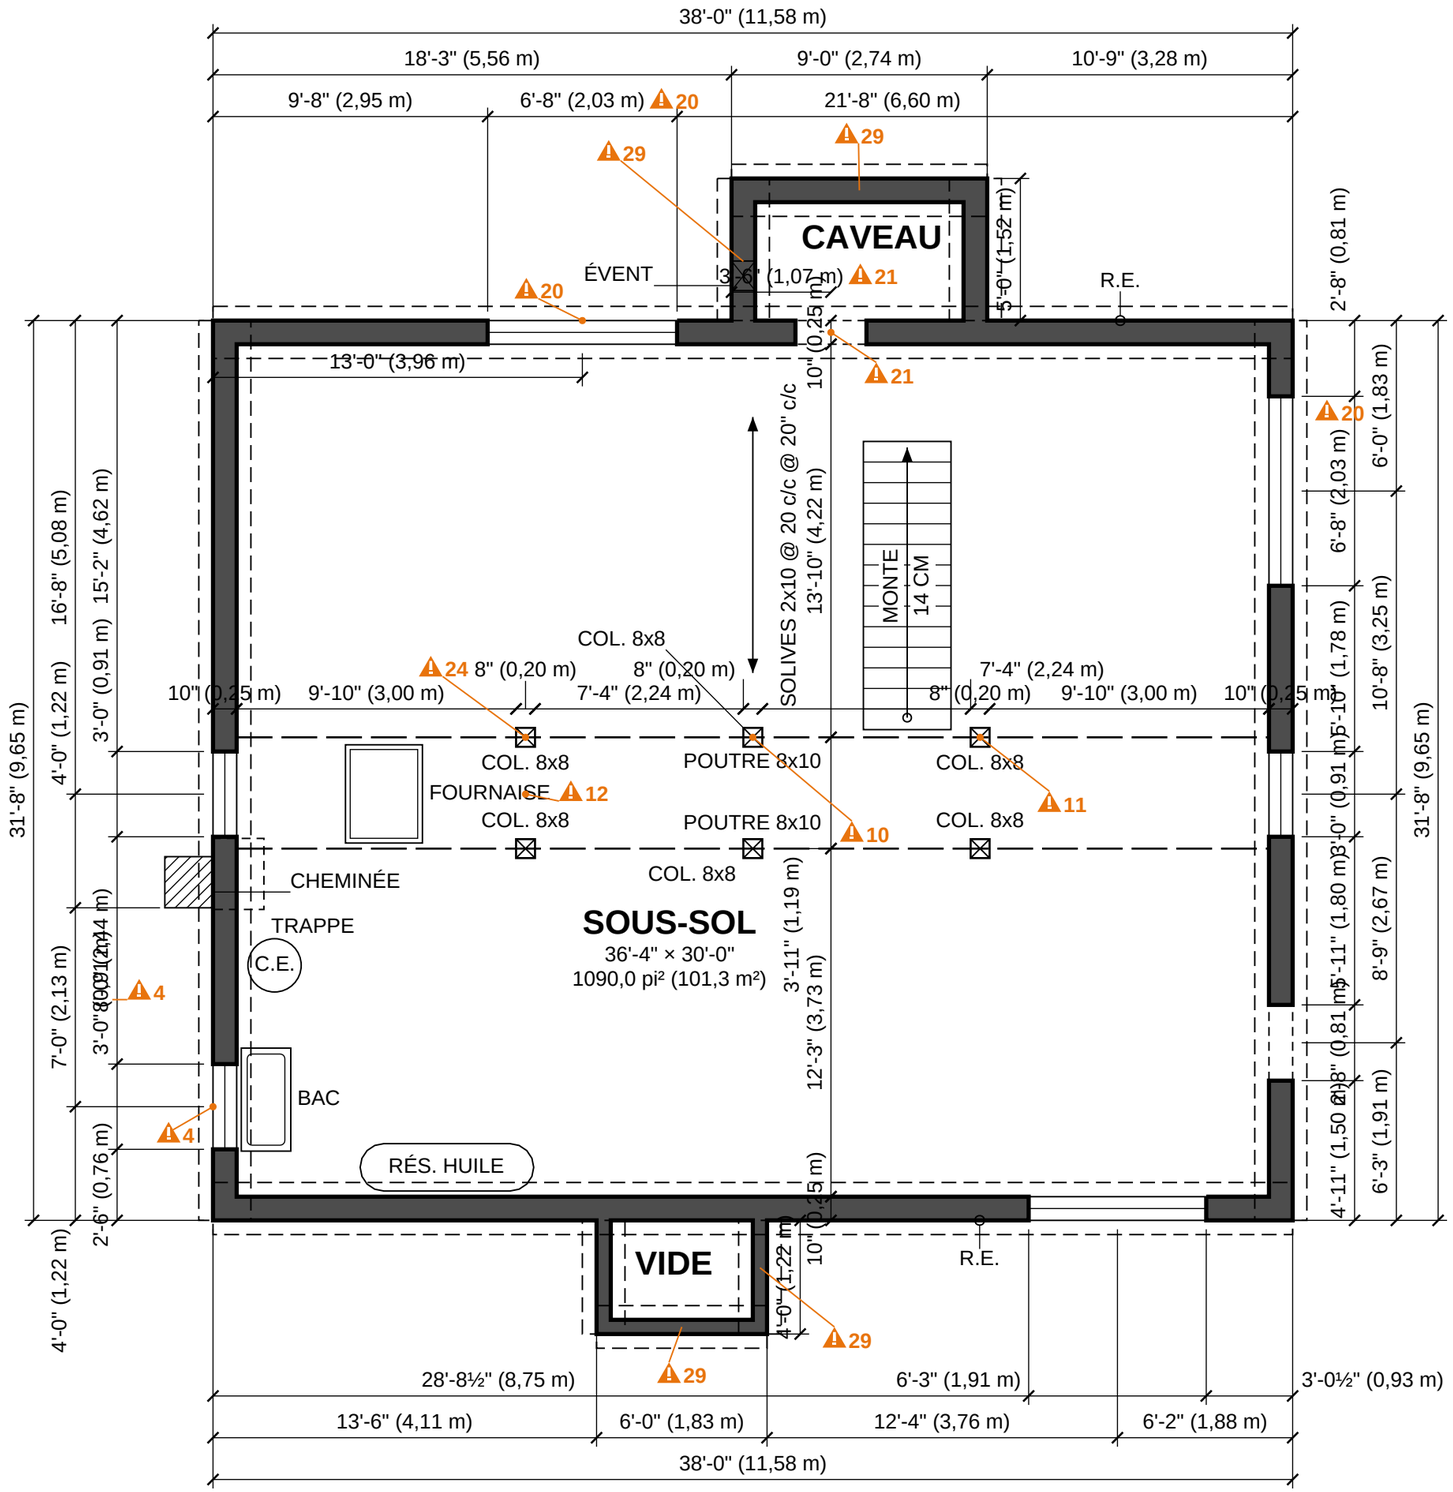


FAÇADE AVANT (RUE)

PROJET

Résidence — 86, avenue Laurier, Baie-Comeau

RELEVÉ DE L'EXISTANT — PRÉLIMINAIRE, À VALIDER SUR PLACE

LÉGENDE

- Mur extérieur / fondation
- Mur intérieur (cloison)
- Poutre (au-dessus)
- Axe porteur d'origine
- Colonne
- Solives (sens)
- ≈ Valeur estimée (mesurée sur l'image)
- ⚠n Voir registre des écarts dans RAPPORT.md
- Cotes en pi-po (métrique en m)

REPÈRES SUR CETTE FEUILLE

⚠4 Cote en conflit cote-SS-017 — Largeur de la fenêtre gauche basse du sous-sol (au-dessus de l'évier à lessive). Lecture 1 « 3'-0" », lecture 2 « 3'-0" », 3e lecture « 3'-0" » (basse). Vignettes : arbitrage/vignettes/d-SS-07_P1.png, arbitrage/vignettes/d-SS-07_P7.png. [ecart-004]

⚠10 Croquis 2016 : « Colonne C4 retirée » (intersection axe C y = 204 × ligne 4 x = 222). Au plan 1957 (P1), la colonne la plus proche est str-SS-C02 à x = 228 (DÉDUIT de la chaîne 9'-10" + 8" + 7'-4") : décalage 6 po entre les deux documents. [ecart-010]

⚠11 Croquis 2016 : « Colonne C6 retirée » (axe C × ligne 6, x = 316). Au plan 1957 : str-SS-C03 à x = 324 (8 po de décalage). [ecart-011]

… liste complète : donnees/verifications.txt

NORD
9.8° (sens horaire depuis +y).
Source : ESTIMÉ (P5)

ÉCHELLE GRAPHIQUE (pi)


0 — 4 — 8 — 12 pi

PHOTOS SOURCES
P1, P7

ÉCHELLE	DATE	RÉVISION
3/16" = 1'-0"	2026-10-29	R0

NIVEAU
SOUS-SOL

FEUILLE
A-100

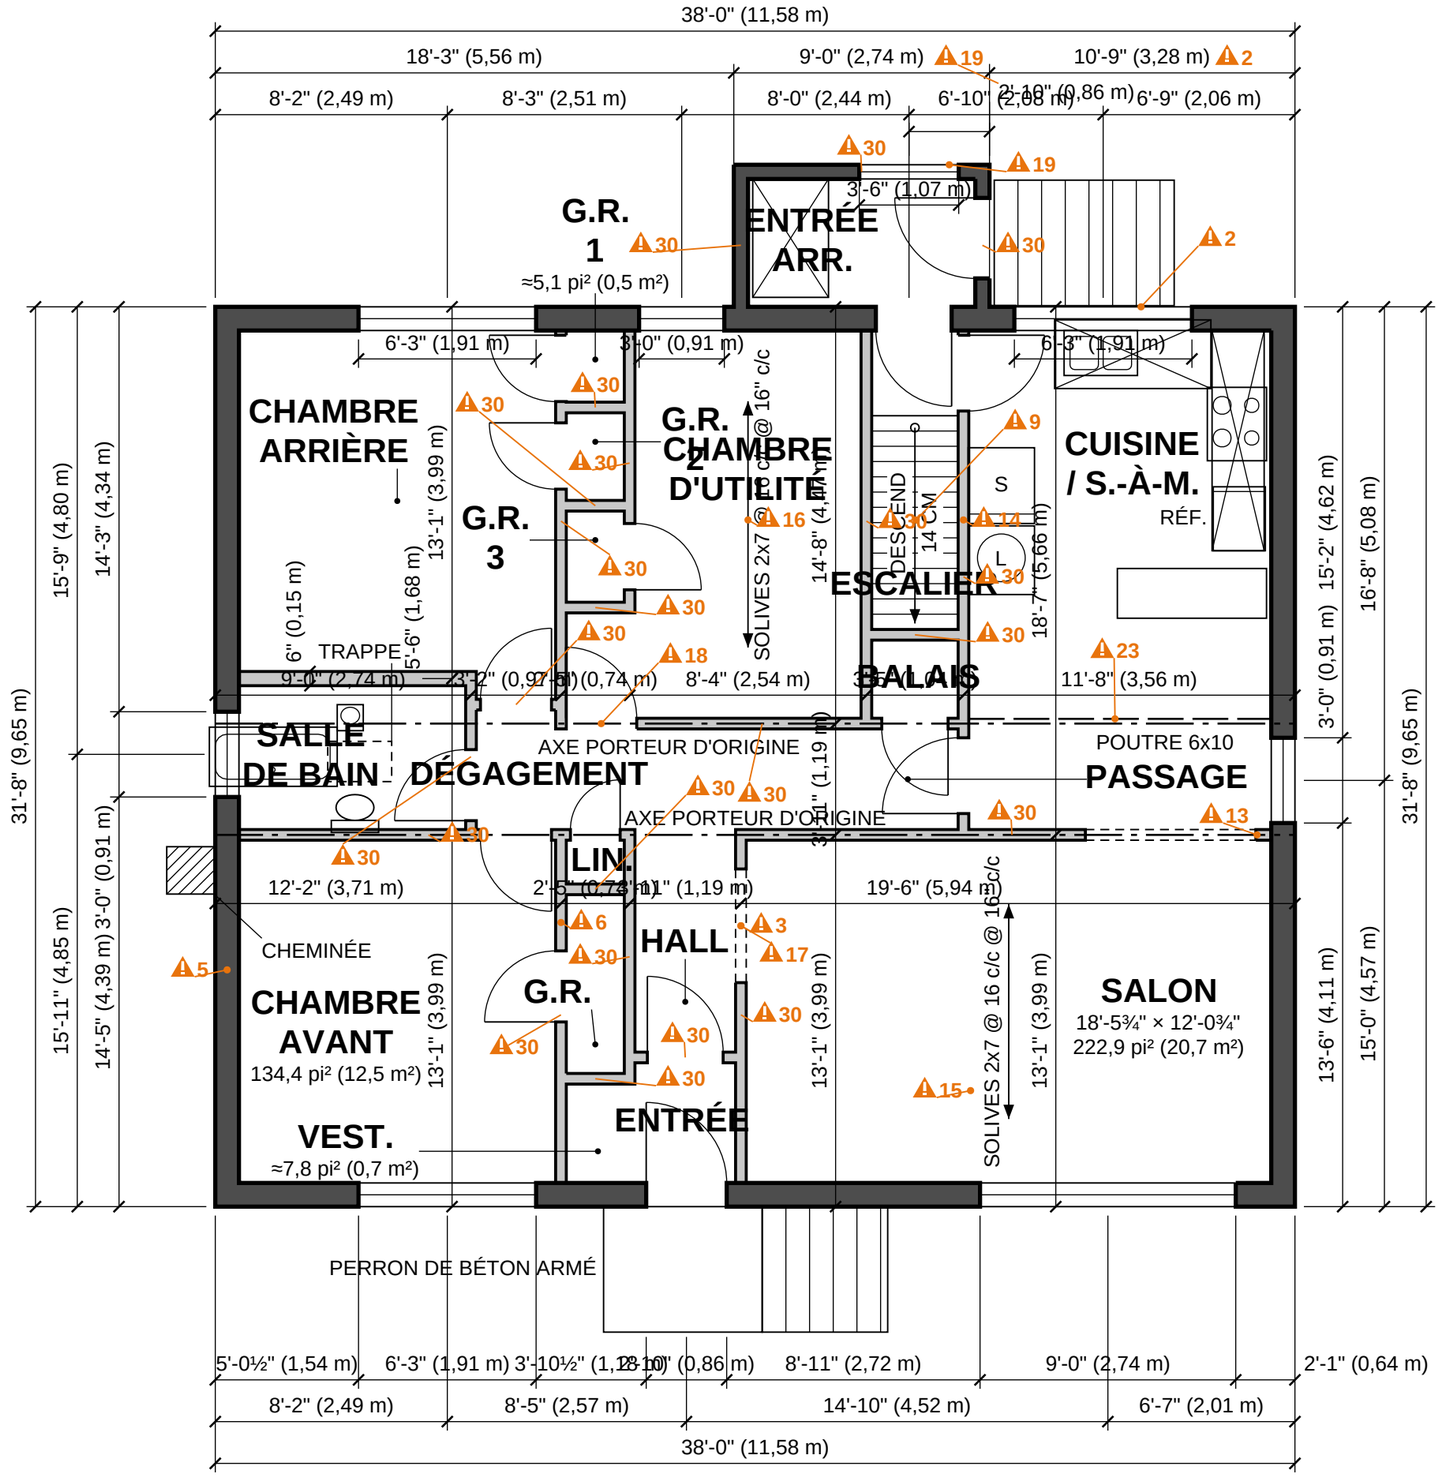

FAÇADE AVANT (RUE)

PROJET

Résidence — 86, avenue Laurier, Baie-Comeau

RELEVÉ DE L'EXISTANT — PRÉLIMINAIRE, À VALIDER SUR PLACE

LÉGENDE

- Mur extérieur / fondation
- Mur intérieur (cloison)
- Poutre (au-dessus)
- Axe porteur d'origine
- Colonne
- Solives (sens)
- ≈ Valeur estimée (mesurée sur l'image)
- ⚠n Voir registre des écarts dans RAPPORT.md
- Cotes en pi-po (métrique en m)

REPÈRES SUR CETTE FEUILLE

⚠2 Cote en conflit cote-RDC-018 — Segment arrière droit 10'-9" / 10'-5" (nu ext. droit de l'entrée arrière → coin arrière droit). Lecture 1 « 10'-9" », lecture 2 « 10-9" », 3e lecture « 10'-5" » (basse). Vignettes : arbitrage/vignettes/d-RDC-03_P4.png, arbitrage/vignettes/d-RDC-03_P6.png. [ecart-002]

⚠3 Cote en conflit cote-RDC-048 — Largeur de l'arche hall / salon : écrit « ARCHE 4'-0" » (2 lectures) contre 6'-0" (3e lecture) ; dessin ≈ 74 po. Lecture 1 « ARCHE 4'-0" », lecture 2 « ARCHE 4'-0" », 3e lecture « ARCHE 6'-0" » (moyenne). Vignettes : arbitrage/vignettes/d-RDC-11_P3.png, arbitrage/vignettes/d-RDC-11_P4.png, arbitrage/vignettes/d-RDC-11_P6.png. [ecart-003]

… liste complète : donnees/verifications.txt

NOTES DU PLAN D'ORIGINE (traduites)

… autres notes : voir maison.json

NORD

9.8° (sens horaire depuis +y).
Source : ESTIMÉ (P5)

ÉCHELLE GRAPHIQUE (pi)

0 4 8 12 pi

PHOTOS SOURCES

P3, P4, P6

ÉCHELLE	DATE	RÉVISION
3/16" = 1'-0"	2026-10-29	R0

NIVEAU

REZ-DE-CHAUSSÉE

FEUILLE

A-101