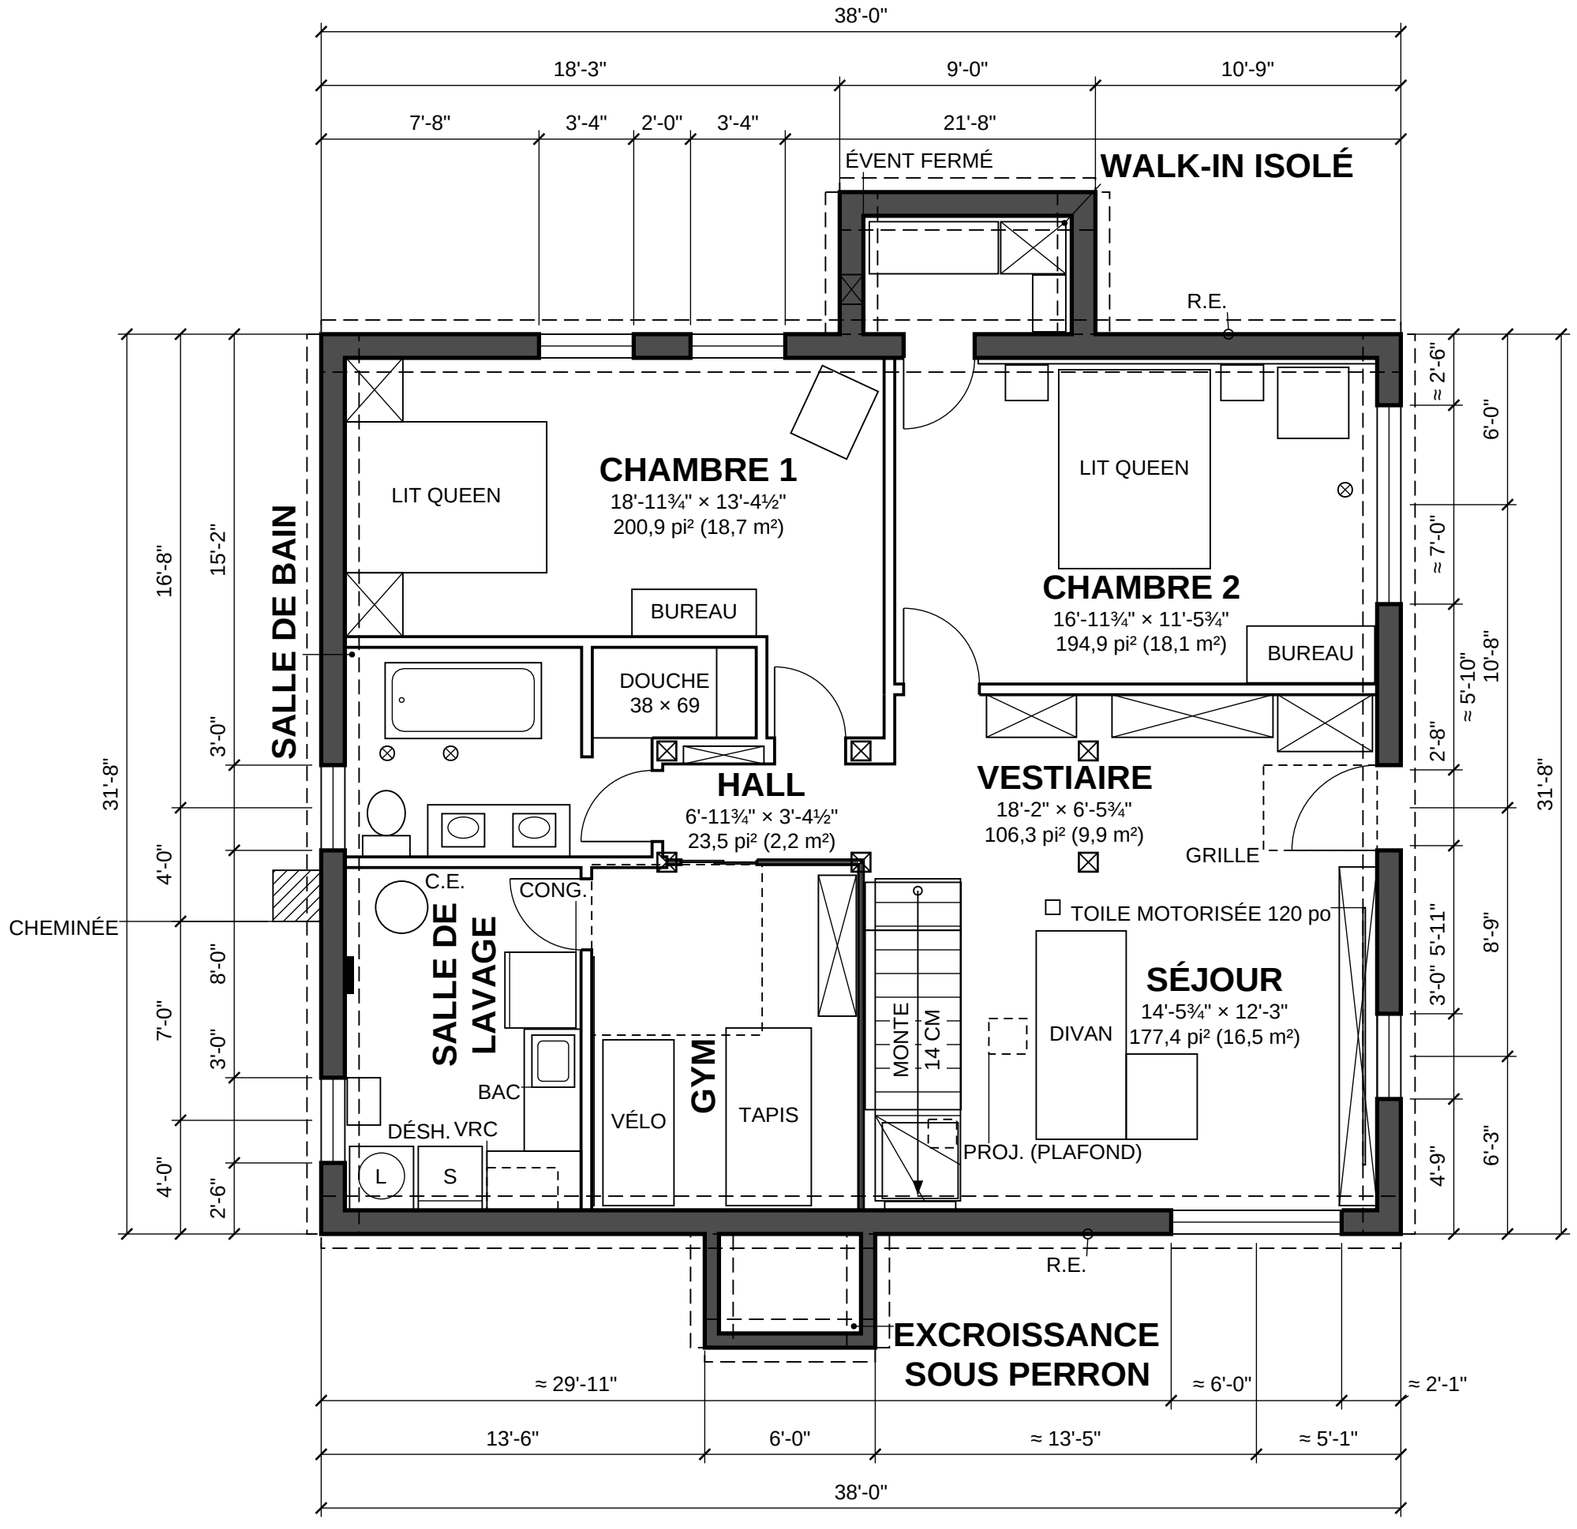


FAÇADE AVANT (RUE)

PROJET

Résidence — 86, avenue Laurier, Baie-Comeau

PROPOSITION MAISON-18 — LES DEUX ÉTAGES : GRANDE ENTRÉE VITRÉE, CHAMBRE KING, BUREAU-GAMING — ESQUISSE À VALIDER

LÉGENDE

- Mur extérieur / fondation
- Mur intérieur existant
- Cloison projetée (nouvelle)
- Cloison vitrée projetée
- Colonne
- ≈ Valeur estimée (mesurée sur l'image)
- ⚠n Voir registre des écarts dans RAPPORT.md
- Cotes en pieds-pouces
- Drain
- Panneau électrique
- Petites pièces : nom seul ; dimensions et superficie dans tableau_pieces.csv

NOTES DE LA PROPOSITION

1. Fenêtres selon la vidéo DAG (allège ≈ 44, tête ≈ 80 po ; chambre 1 : allège ≈ 40) ; congélateur au lavage.
2. Hall : mur épais sous la poutre arrière (colonnes cachées) ; chambre 1 et salle de bain agrandies ; fenêtres d'évacuation à vérifier.
3. Walk-in (ancien caveau) : isolé, évents fermés, chauffé ; porte dérobée dans le mur de chêne de la chambre 2.
4. Escalier : banc-cabane bas (≤ 26 po) dessous ; vides entre les marches (5½ po) à valider avec des enfants.

… autres notes : voir maison.json

NORD

N

9,8° (sens horaire depuis +y).
Source : ESTIMÉ (P7)

ÉCHELLE GRAPHIQUE (pi)

0 4 8 12 pi

PHOTOS SOURCES

P2, P3


ÉCHELLE	DATE	RÉVISION
3/16" = 1'-0"	2026-11-01	A

NIVEAU

SOUS-SOL PROPOSÉ

FEUILLE

P-129

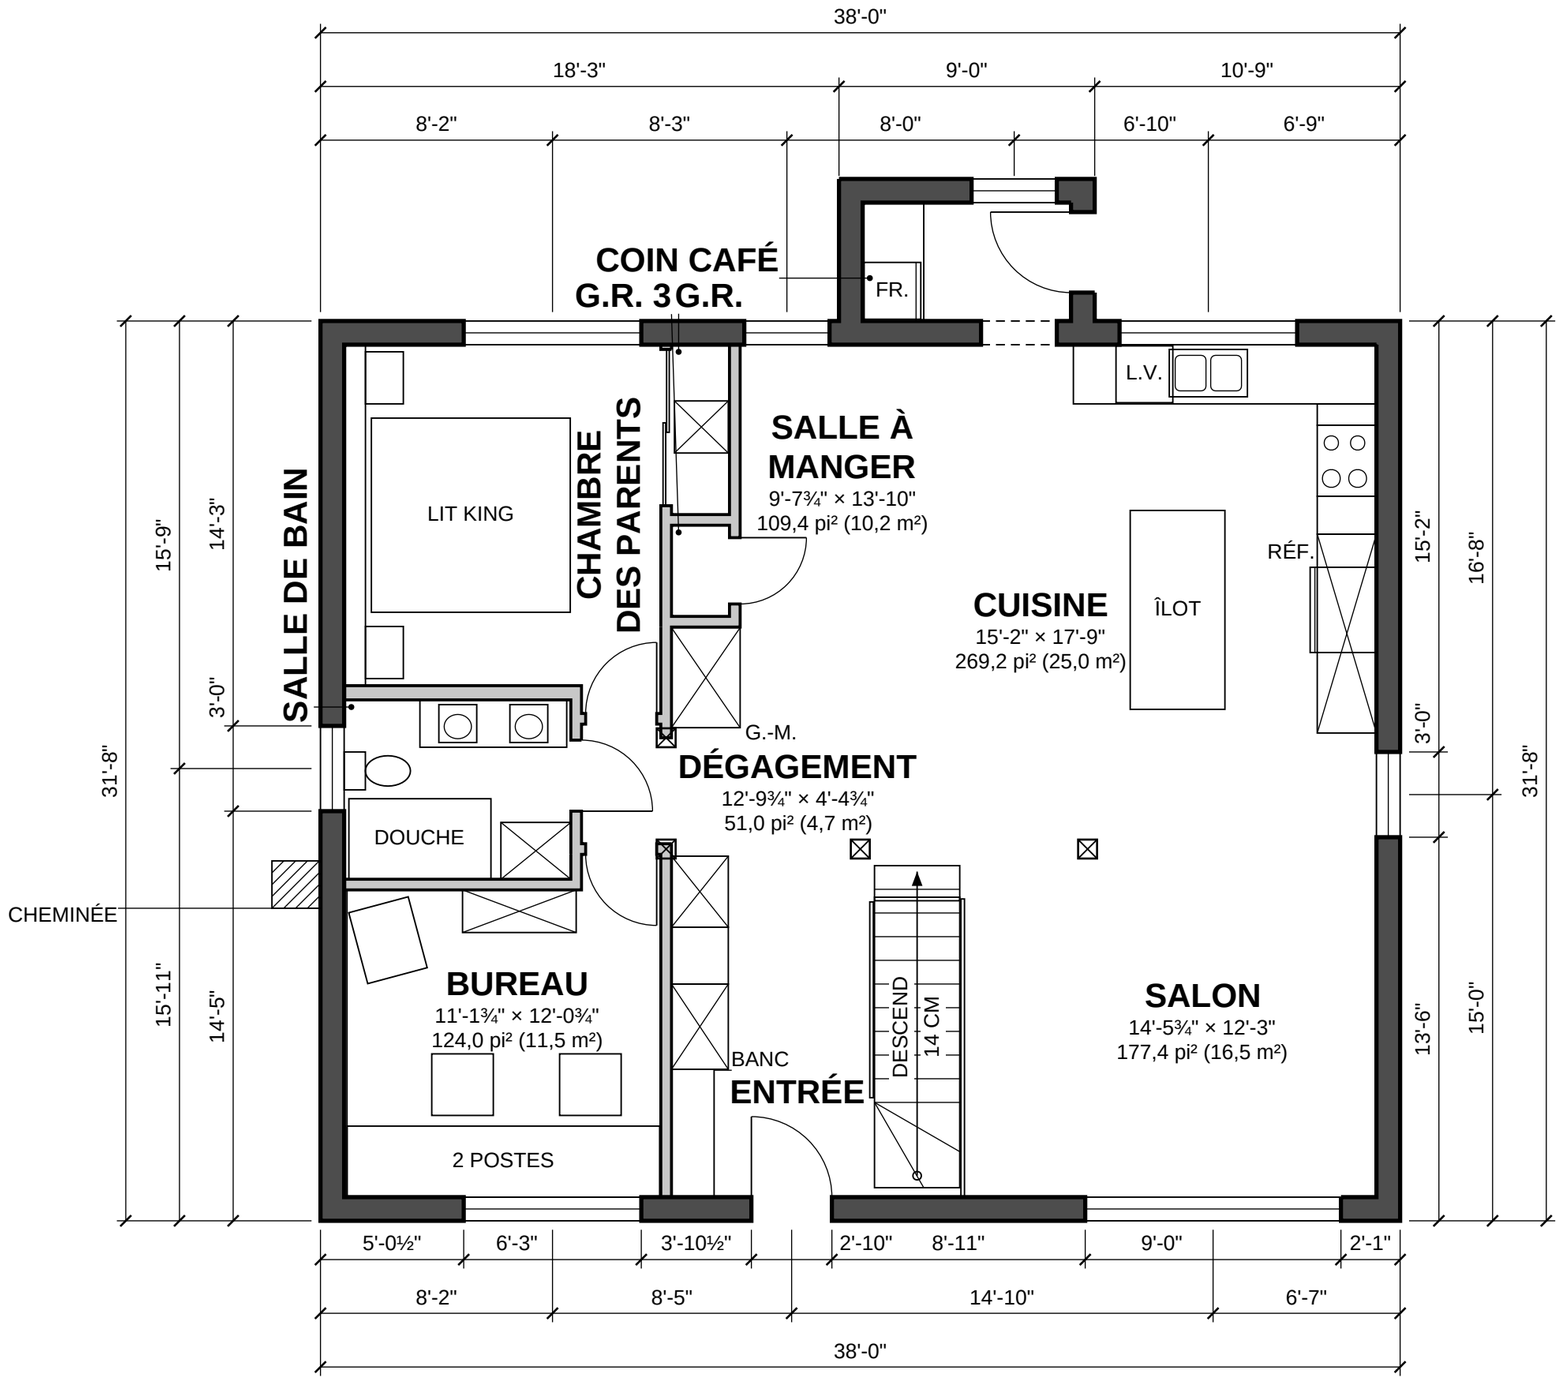

FAÇADE AVANT (RUE)

PROJET

Résidence — 86, avenue Laurier, Baie-Comeau

PROPOSITION MAISON-18 — LES DEUX ÉTAGES : GRANDE ENTRÉE VITRÉE, CHAMBRE KING, BUREAU-GAMING — ESQUISSE À VALIDER

LÉGENDE

- Mur extérieur / fondation
- Mur intérieur (cloison)
- ⊠ Colonne
- ≈ Valeur estimée (mesurée sur l'image)
- ⚠n Voir registre des écarts dans RAPPORT.md
- Cotes en pieds-pouces
- Petites pièces : nom seul ; dimensions et superficie dans tableau_pieces.csv

NOTES DE LA PROPOSITION

1. Esquisse sur le relevé photo RDC-01 (le reste est l'existant ; cotes à mesurer) ; fenêtres selon la vidéo DAG (salon : allège ≈ 12 po).
2. Grande entrée ouverte : garde-robes du hall enlevées ; escalier entouré d'un garde-corps de verre.
3. Escalier vers le sous-sol : trémie ≈ 3 × 10 pi ; échappée ≈ 1,96 m à vérifier ; garde-corps de 42 po conseillé.
4. Chambre des parents : lit king, mur de tête en bois de grange, garde-robes réunies à portes coulissantes.
5. Bureau-gaming (ancienne chambre avant) : 2 postes face à la fenêtre avant.
6. Poutre et appuis de l'ancienne cloison hall/salon, coupe-feu entre logements : à valider avec la Ville et un professionnel.

NORD

N

9,8° (sens horaire depuis +y).
Source : ESTIMÉ (P7)

ÉCHELLE GRAPHIQUE (pi)

0 — 4 — 8 — 12 pi

PHOTOS SOURCES

photos 01 à 15 du 2026-11-01

ÉCHELLE	DATE	RÉVISION
3/16" = 1'-0"	2026-11-01	A

NIVEAU	FEUILLE
REZ-DE-CHAUSSÉE PROPOSÉ	P-130