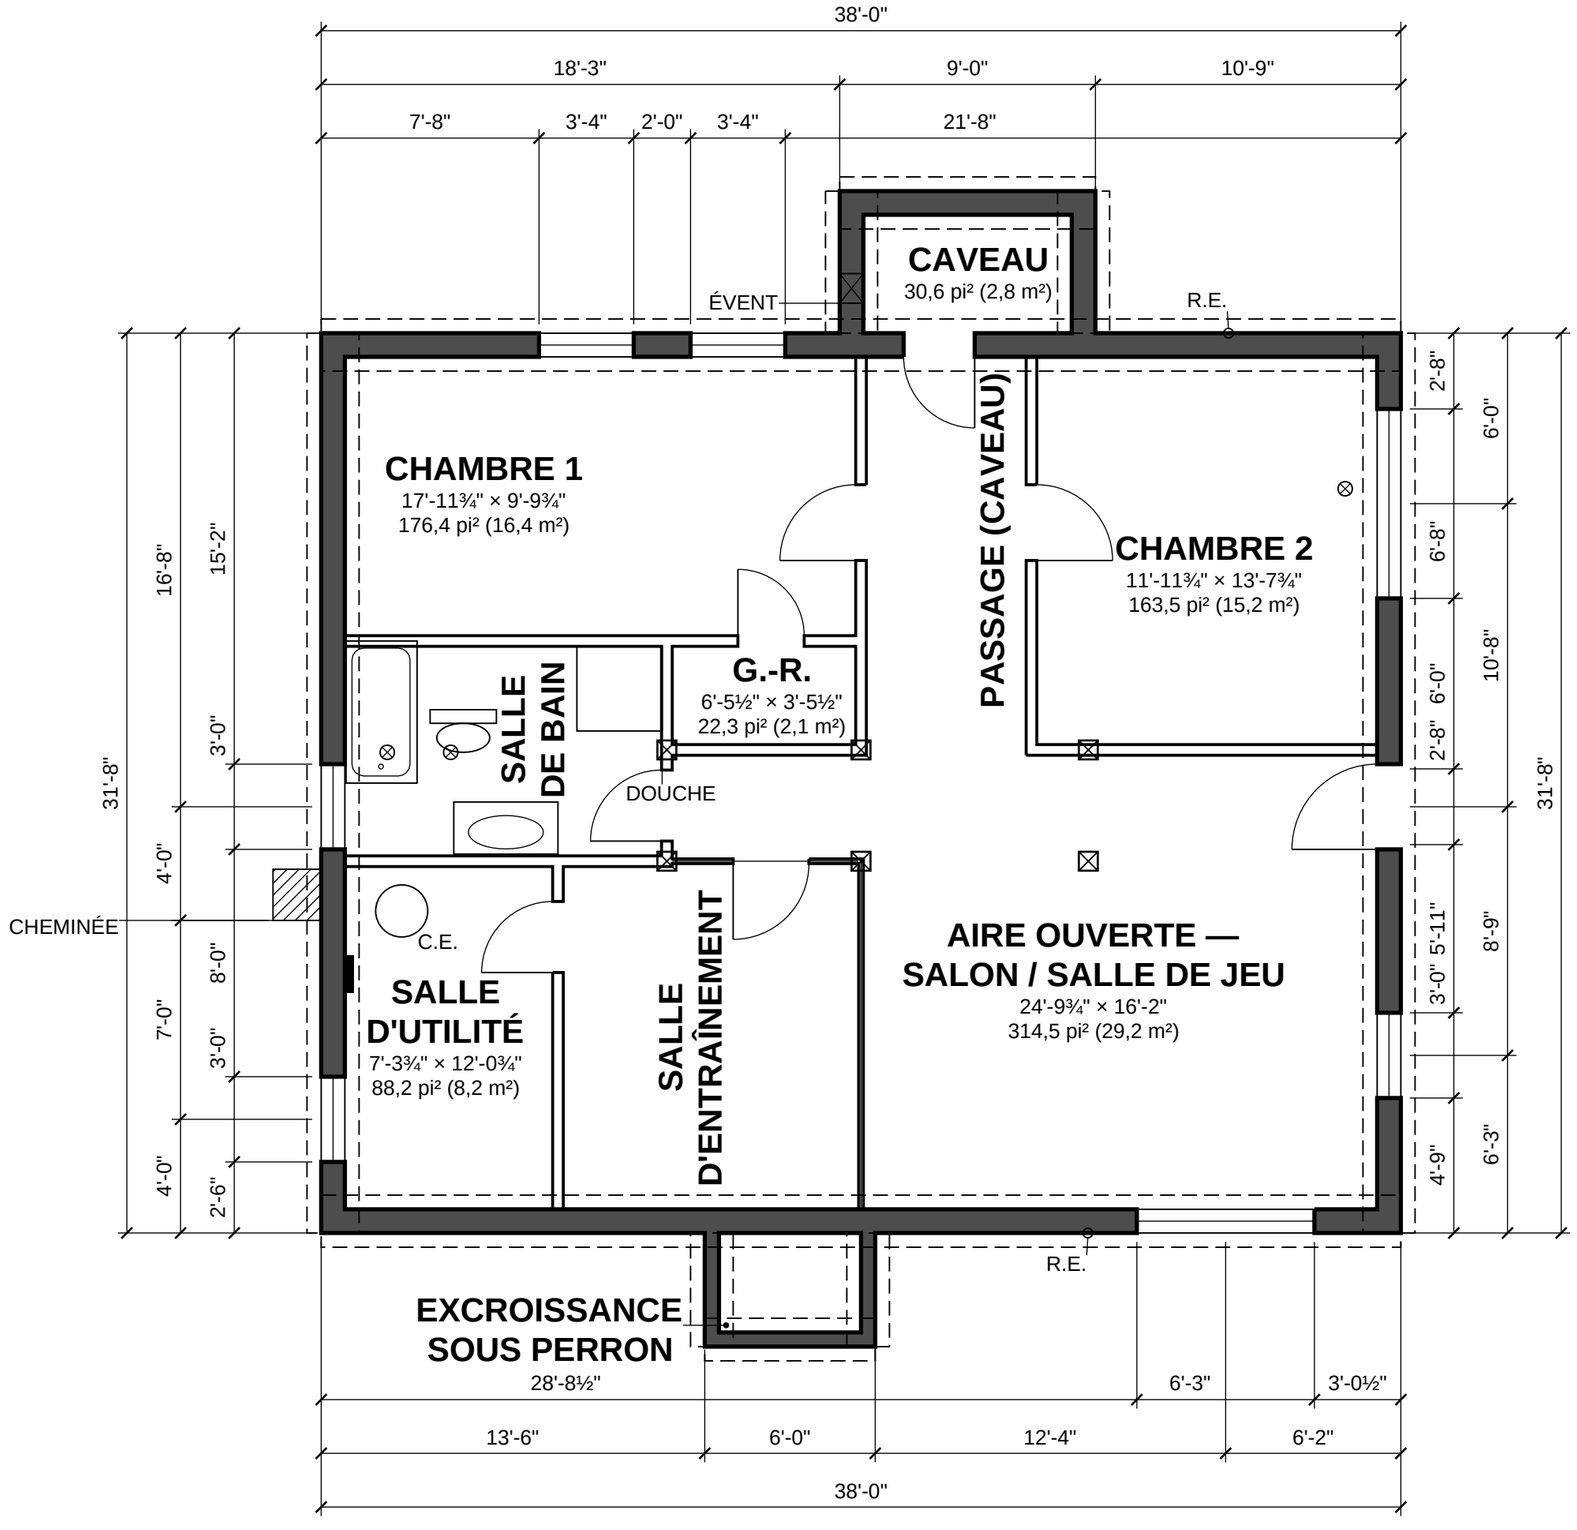

FAÇADE AVANT (RUE)

PROJET

Résidence — 86, avenue Laurier, Baie-Comeau

PROPOSITION SS-02 — AIRE OUVERTE, SALLE D'ENTRAÎNEMENT VITRÉE — ESQUISSE À VALIDER

LÉGENDE

- Mur extérieur / fondation
- Mur intérieur existant
- Cloison projetée (nouvelle)
- Cloison vitrée projetée
- Colonne
- ≈ Valeur estimée (mesurée sur l'image)
- ⚠n Voir registre des écarts dans RAPPORT.md
- Cotes en pieds-pouces
- Drain
- Panneau électrique
- Petites pièces : nom seul ; dimensions et superficie dans tableau_pieces.csv

NOTES DE LA PROPOSITION

1. Esquisse : cloisons, portes et équipements de salle de bain projetés ; tout le reste est l'existant (plans de base R0).
2. Aire ouverte : salon / salle de jeu ouvert sur le corridor ; salle d'entraînement fermée par des cloisons vitrées à cadre noir et une porte vitrée.
3. Les murs du corridor passent sur les deux poutres et les six colonnes 8"x8" existantes.
4. Fenêtres des chambres à vérifier pour l'évacuation (dimension et hauteur d'allège) ; hauteur sous poutres à mesurer.

NORD

N

9,8° (sens horaire depuis +y).
Source : ESTIMÉ (P7)

ÉCHELLE GRAPHIQUE (pi)

0 4 8 12 pi

PHOTOS SOURCES

P2, P3

ÉCHELLE	DATE	RÉVISION
3/16" = 1'-0"	2026-10-29	A

NIVEAU

SOUS-SOL PROPOSÉ

FEUILLE

P-101