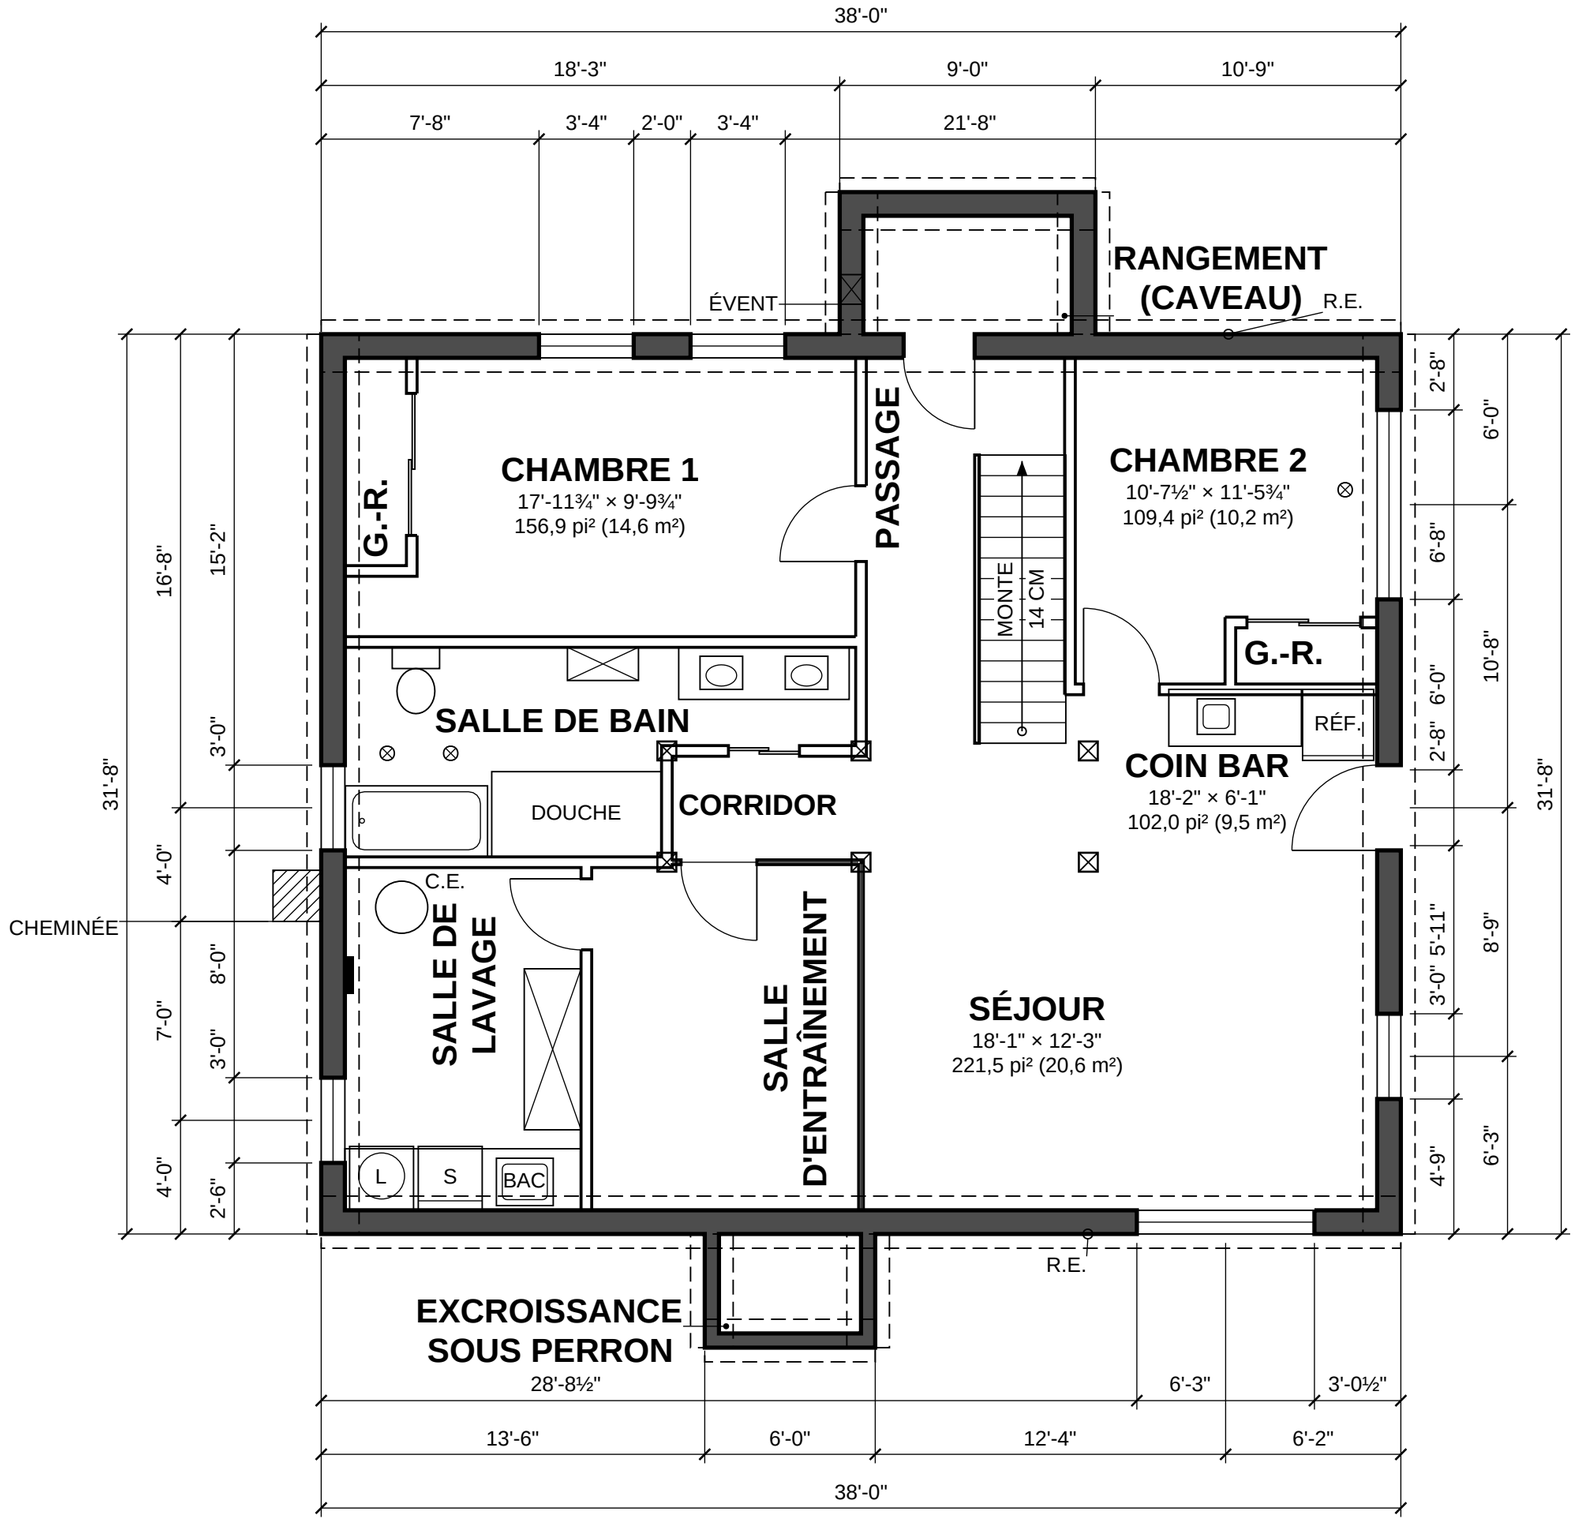

FAÇADE AVANT (RUE)

PROJET

Résidence — 86, avenue Laurier, Baie-Comeau

PROPOSITION SS-05 — SALLE DE BAIN REVUE, MATÉRIAUX — ESQUISSE À VALIDER

LÉGENDE

- Mur extérieur / fondation
- Mur intérieur existant
- Cloison projetée (nouvelle)
- Cloison vitrée projetée
- ⊠ Colonne
- ≈ Valeur estimée (mesurée sur l'image)
- ⚠n Voir registre des écarts dans RAPPORT.md
- Cotes en pieds-pouces
- ⊗ Drain
- ▬ Panneau électrique
- Petites pièces : nom seul ; dimensions et superficie dans tableau_pieces.csv

NOTES DE LA PROPOSITION

1. Esquisse : cloisons, portes, escalier, bar et appareils projetés ; le reste est l'existant (base R0).
2. Escalier de 14 c.m. à l'emplacement de 1957 : trémie à rouvrir au rez-de-chaussée ; giron et échappée à valider.
3. Salle de bain : toilette et bain déplacés, drains existants ignorés (tranchée dans la dalle).
4. Coin bar : lavabo de bar à ~9 pi du drain de la chambre 2 (raccord à prévoir).
5. Salle de lavage : panneau et chauffe-eau en place, 36 po libres devant le panneau.
6. Évacuation des chambres, hauteur sous poutres, coupe-feu à valider.

NORD

N

9,8° (sens horaire depuis +y).
Source : ESTIMÉ (P7)

ÉCHELLE GRAPHIQUE (pi)

0 4 8 12 pi

PHOTOS SOURCES

P2, P3

ÉCHELLE	DATE	RÉVISION
3/16" = 1'-0"	2026-10-29	A

NIVEAU

SOUS-SOL PROPOSÉ

FEUILLE

P-104