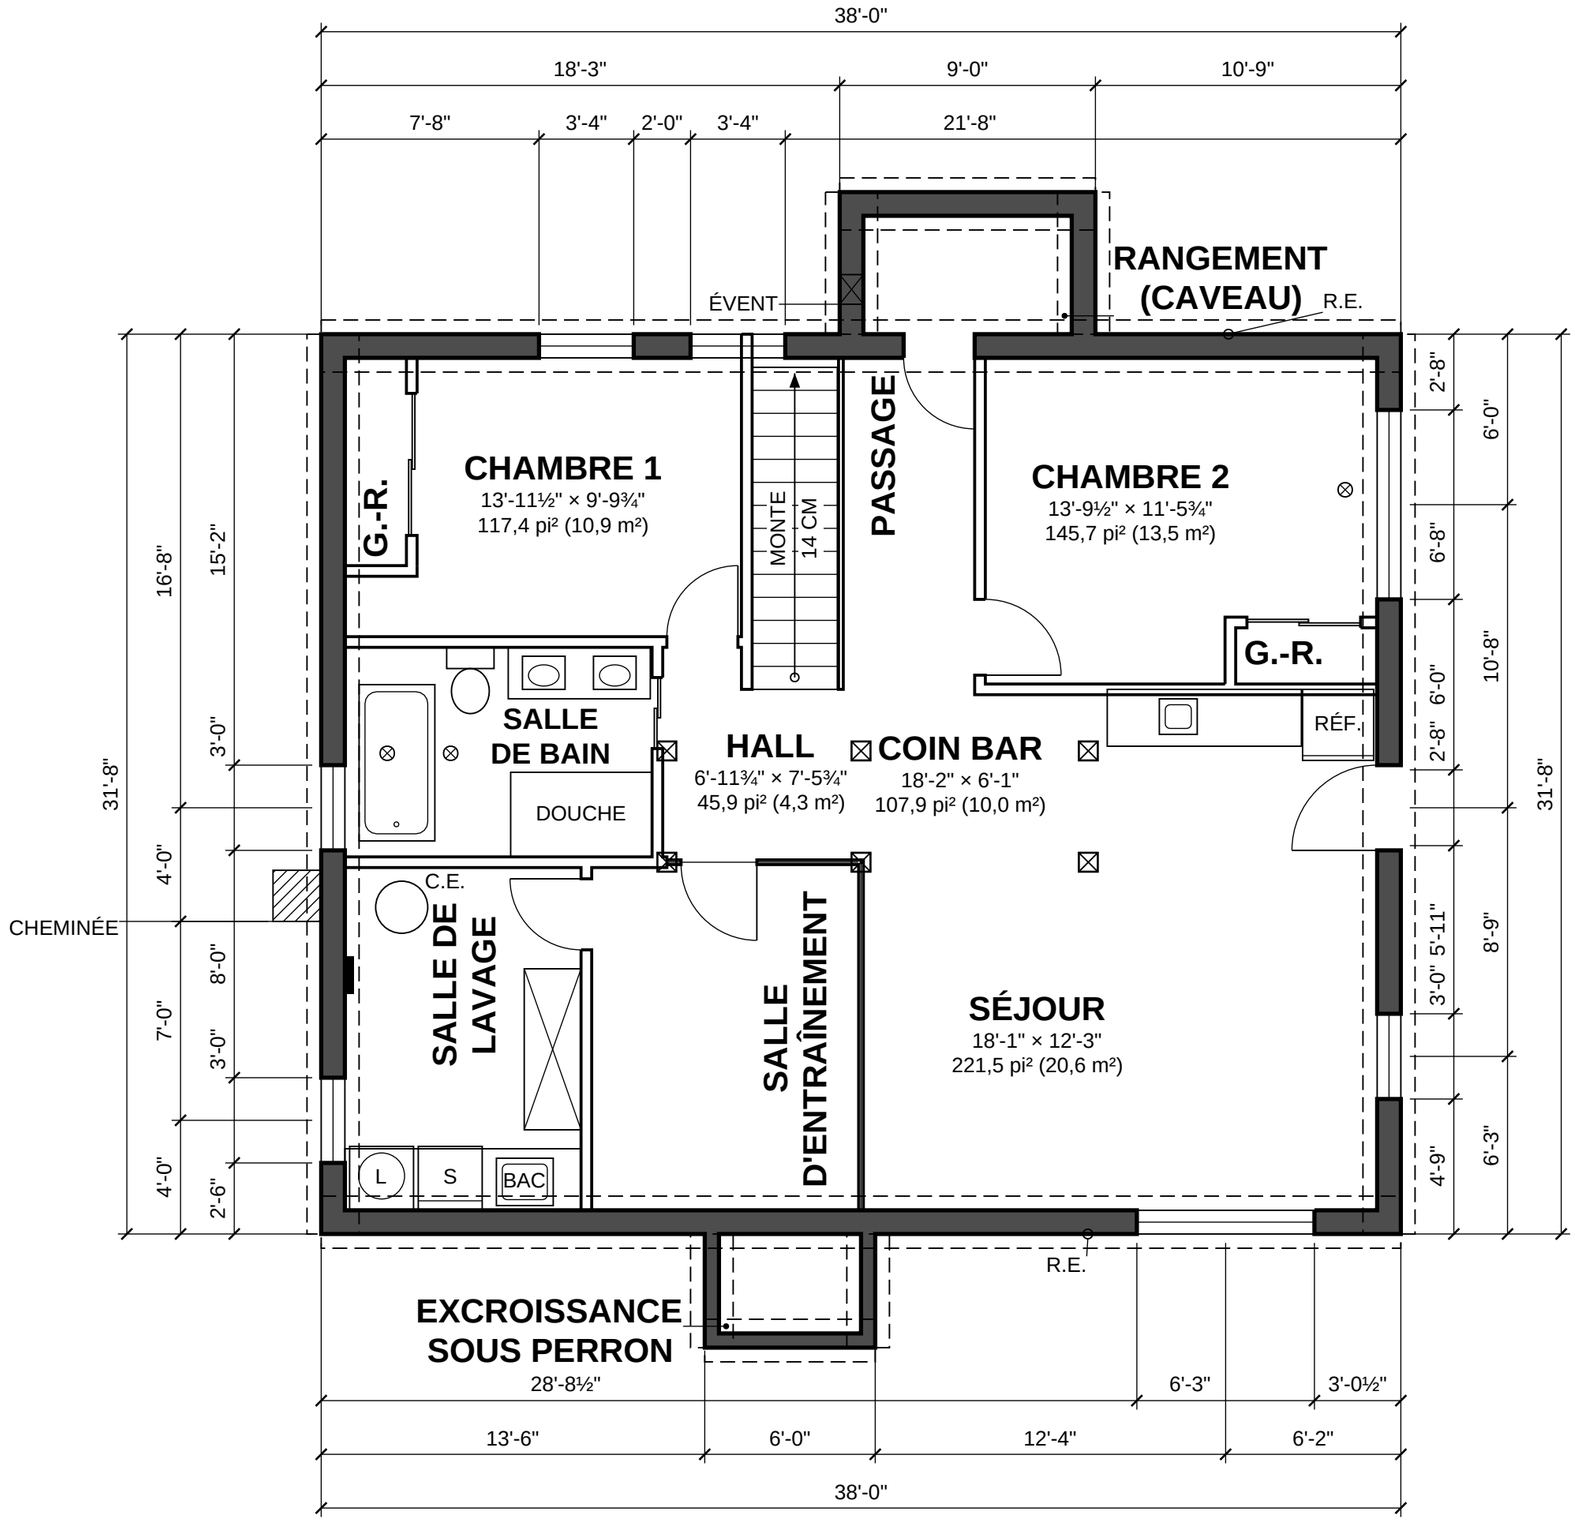


FAÇADE AVANT (RUE)

PROJET

Résidence — 86, avenue Laurier, Baie-Comeau

PROPOSITION SS-06 — NOUVEL ESCALIER, SOUS-SOL REPENSÉ — ESQUISSE À VALIDER

LÉGENDE

- Mur extérieur / fondation
- Mur intérieur existant
- Cloison projetée (nouvelle)
- Cloison vitrée projetée
- ⊠ Colonne
- ≈ Valeur estimée (mesurée sur l'image)
- ⚠n Voir registre des écarts dans RAPPORT.md
- Cotes en pieds-pouces
- ⊗ Drain
- ▬ Panneau électrique
- Petites pièces : nom seul ; dimensions et superficie dans tableau_pieces.csv

NOTES DE LA PROPOSITION

1. Esquisse : cloisons, portes, escalier, bar et appareils projetés ; le reste est l'existant (base R0).
2. Escalier de 14 c.m. au nouvel emplacement (voir P-106) : trémie à ouvrir, giron et échappée à valider.
3. Fenêtre arrière de la chambre 1 coupée par l'escalier : la réduire ou la condamner (à décider).
4. Salle de bain : bain autoportant et toilette déplacés, drains existants ignorés (tranchée).
5. Coin bar : lavabo de bar à ~6 pi du drain de la chambre 2 (raccord à prévoir).
6. Évacuation des chambres, hauteur sous poutres, coupe-feu à valider.

NORD
9,8° (sens horaire depuis +y).
Source : ESTIMÉ (P7)


ÉCHELLE GRAPHIQUE (pi)

0 — 4 — 8 — 12 pi

PHOTOS SOURCES
P2, P3

ÉCHELLE	DATE	RÉVISION
3/16" = 1'-0"	2026-10-29	A

NIVEAU	FEUILLE
SOUS-SOL PROPOSÉ	P-105

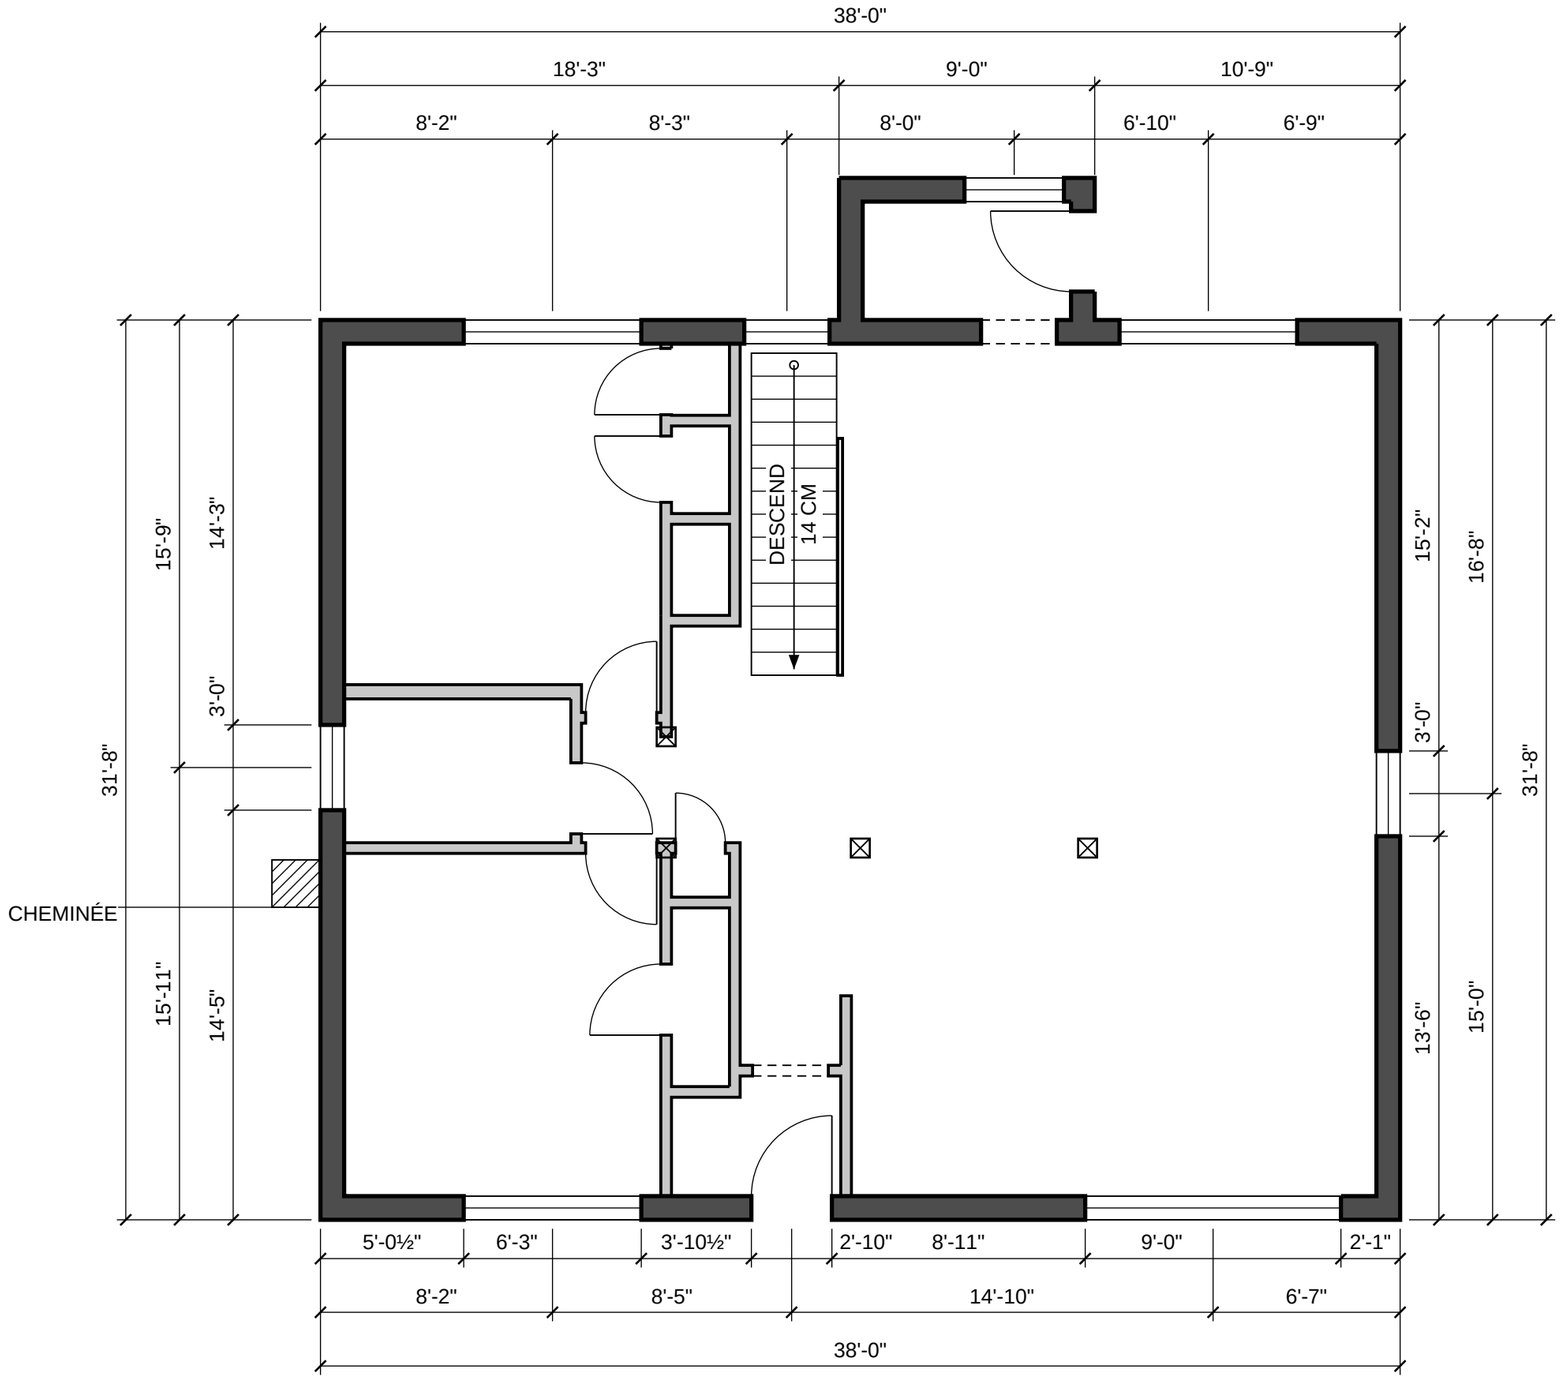

FAÇADE AVANT (RUE)

PROJET

Résidence — 86, avenue Laurier, Baie-Comeau

PROPOSITION SS-06 — NOUVEL ESCALIER, SOUS-SOL REPENSÉ — ESQUISSE À VALIDER

LÉGENDE

- Mur extérieur / fondation
- Mur intérieur existant
- Cloison projetée (nouvelle)
- ⊠ Colonne
- ≈ Valeur estimée (mesurée sur l'image)
- ⚠n Voir registre des écarts dans RAPPORT.md
- Cotes en pieds-pouces

NOTES DE LA PROPOSITION

1. Escalier projeté (même emplacement qu'au sous-sol) : trémie d'environ 3 × 9 pi à ouvrir dans le plancher.
2. Entrée par la droite, au fond (trois marches tournantes) ; garde en lattes de chêne côté salle à manger.
3. Porte de garde-robe qui donnait sur l'escalier enlevée : à refaire du côté de la chambre.
4. Fenêtre arrière au-dessus du haut de l'escalier ; séparation coupe-feu entre logements à valider.

NORD

N

9,8° (sens horaire depuis +y).
Source : ESTIMÉ (P7)

ÉCHELLE GRAPHIQUE (pi)

0 — 4 — 8 — 12 pi

PHOTOS SOURCES

P4, P5, P6

ÉCHELLE	DATE	RÉVISION
3/16" = 1'-0"	2026-10-29	A

NIVEAU

RDC PROPOSÉ

FEUILLE

P-106